

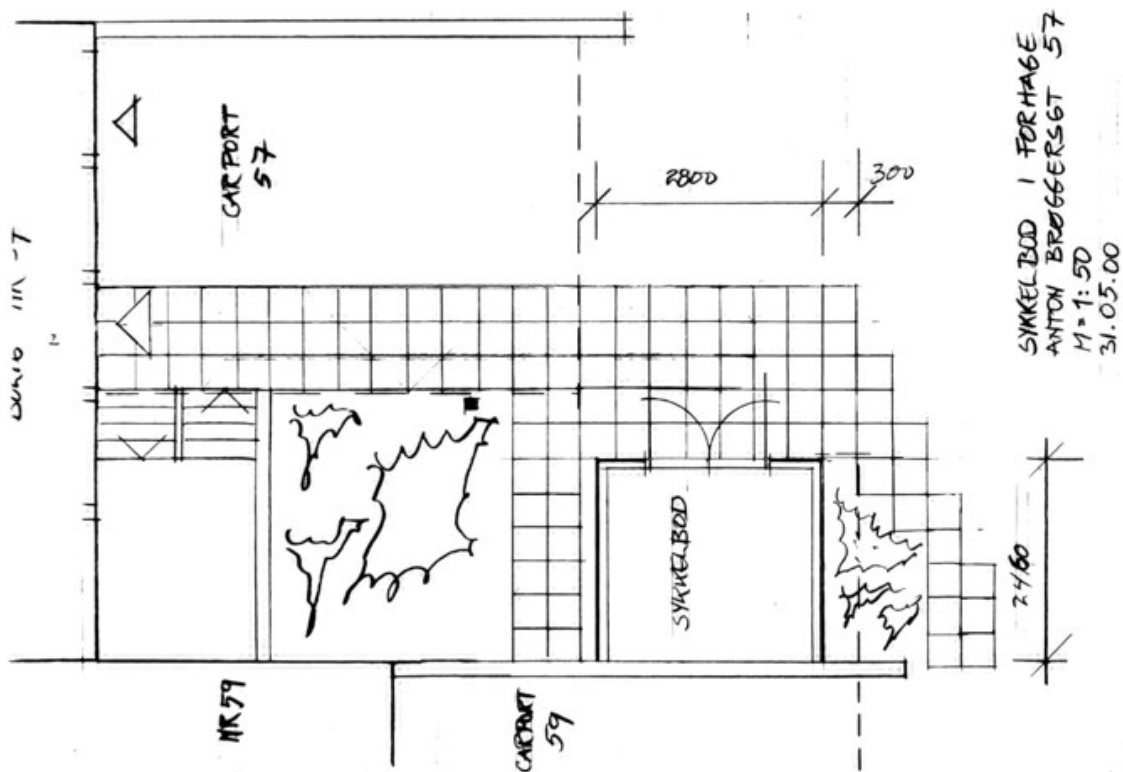


Vedlegg 3

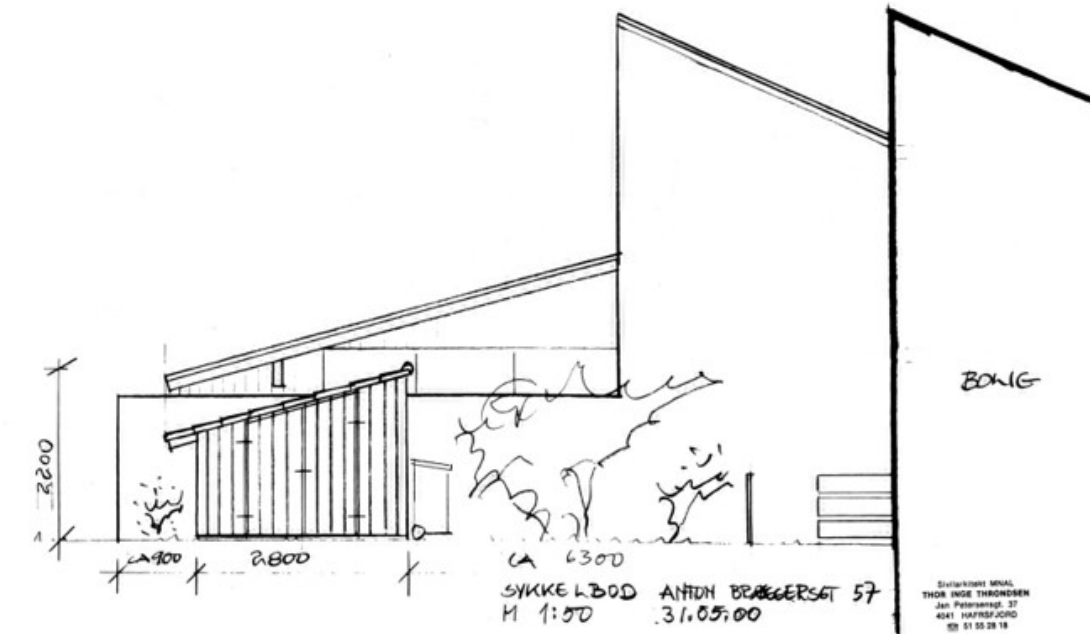


Løsning for bod på inngangsside

STAVANGER KOMMUNE	
Sentralarkivet	
Dato:	09 JUL 2012
S.nr.	J.nr.
Avd.	Arkivkode

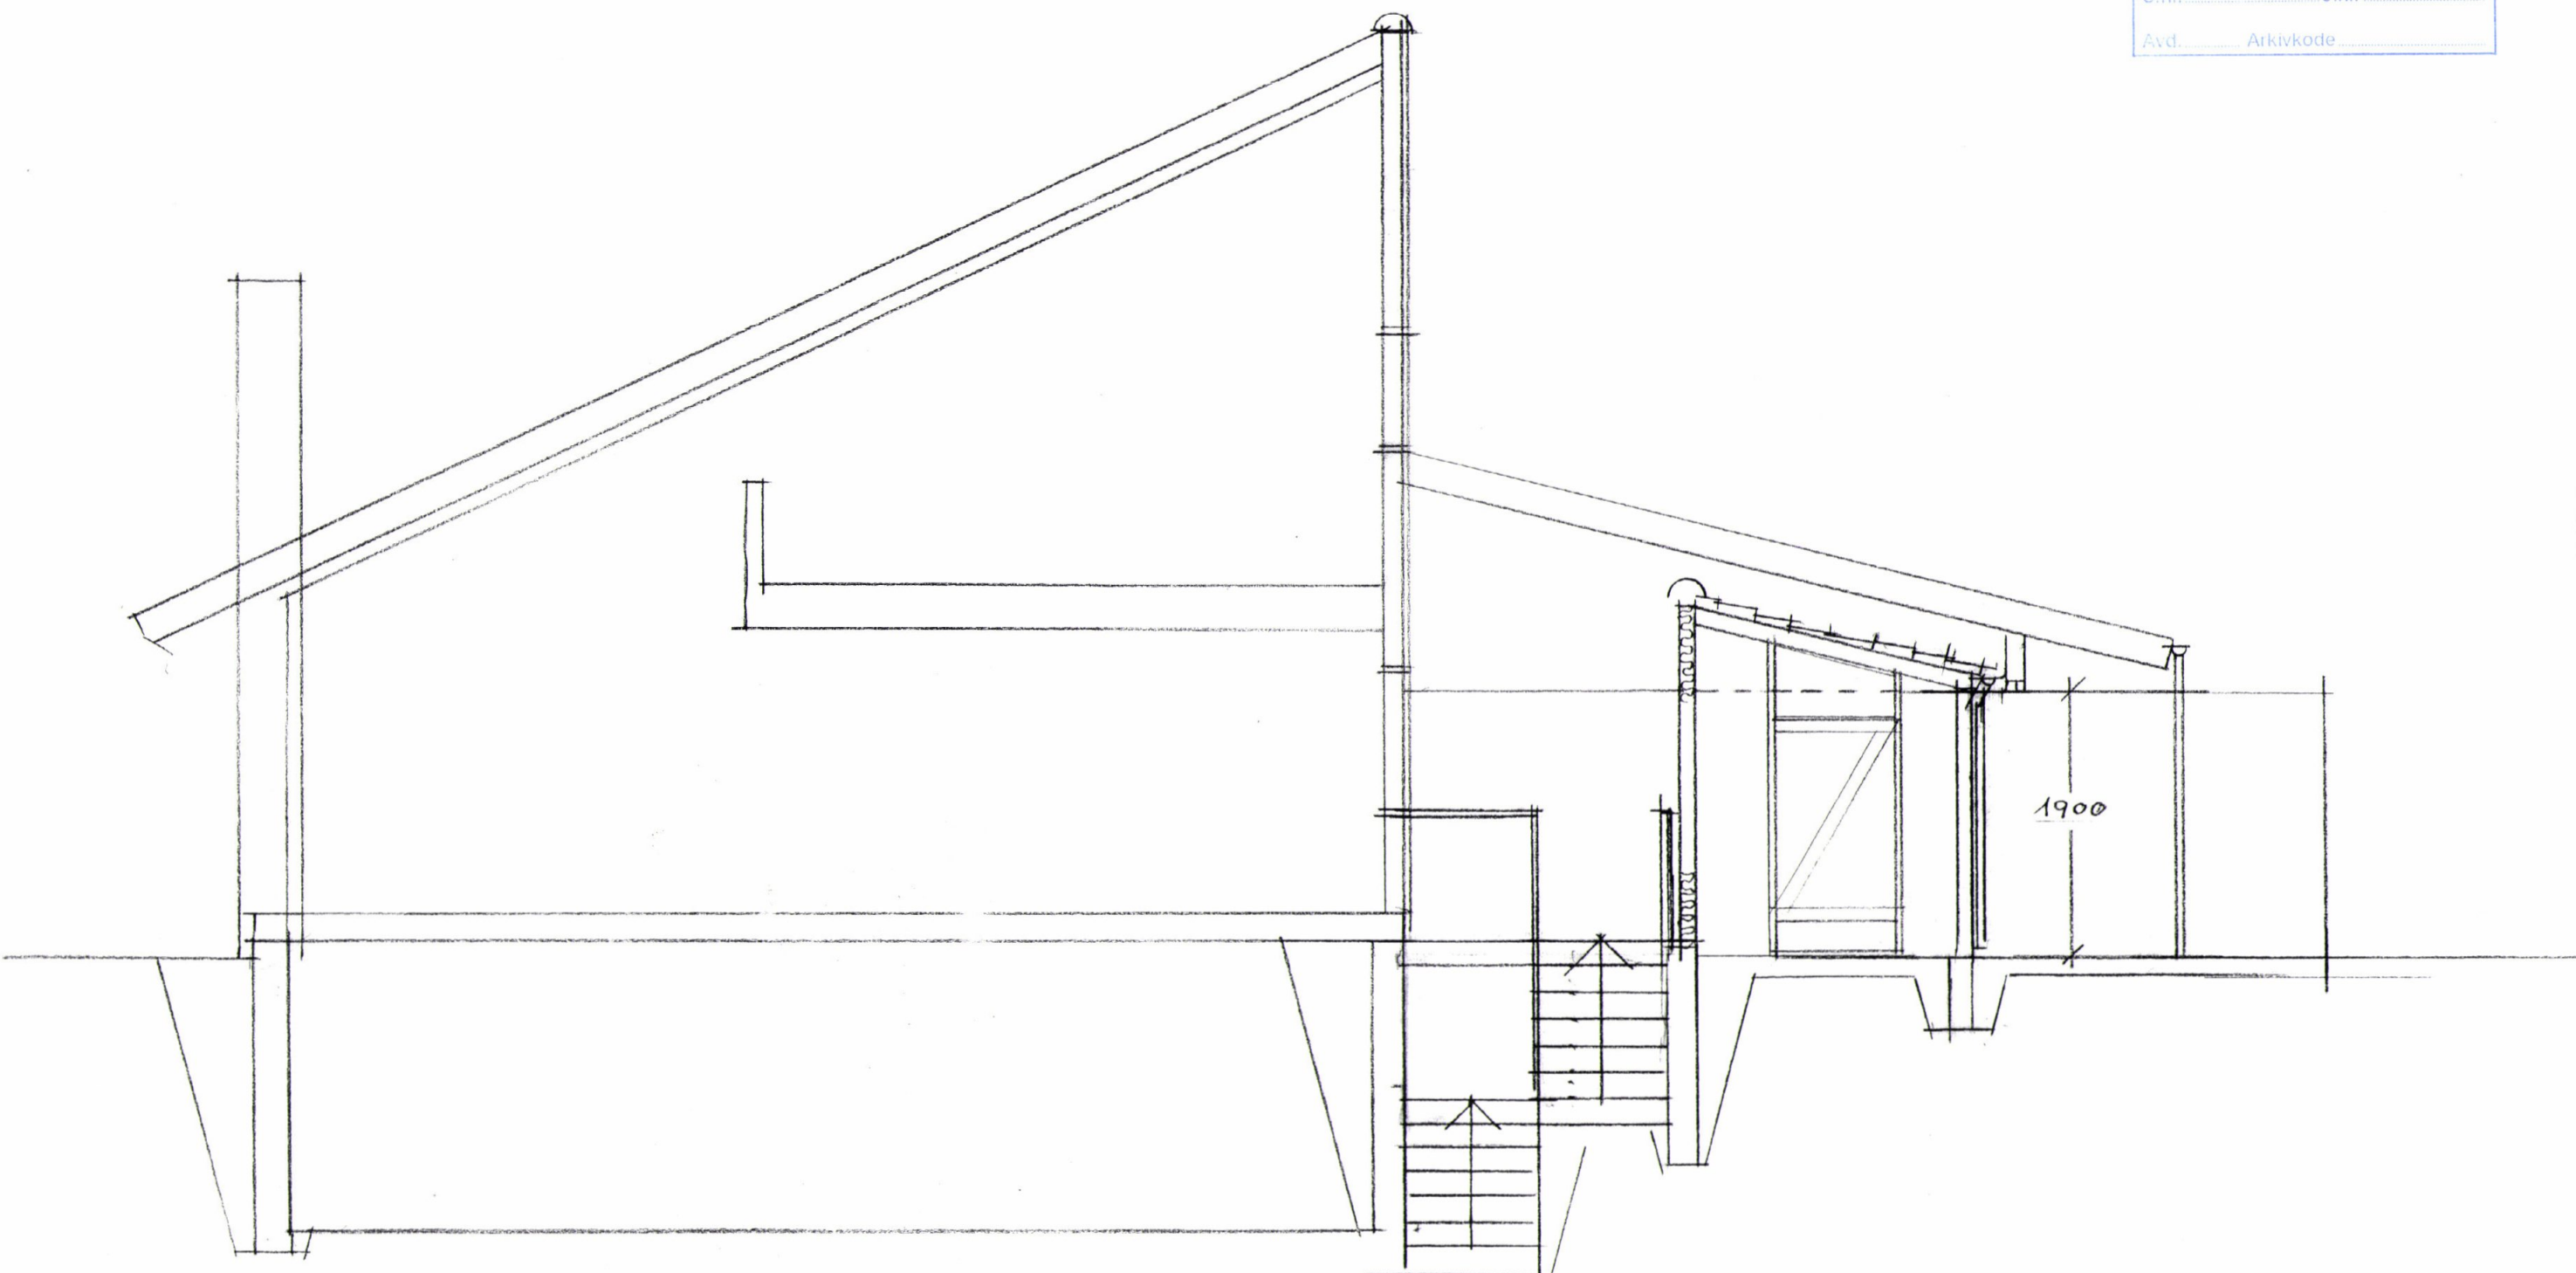

JAN PETERSENSGT. OG ANTON BRØCCERSGT.
 SNITT AV LITEN BOD PÅ ADKOMST SIDE MÅL 1:50 01
 DATO 06-12-11 ARK. THOR THOMASSEN

STAVANGER KOMMUNE	
Sentralarkivet	
Dato:	09 JUL 2012
Snr:	J.nr.
Ans:	Arkivkode

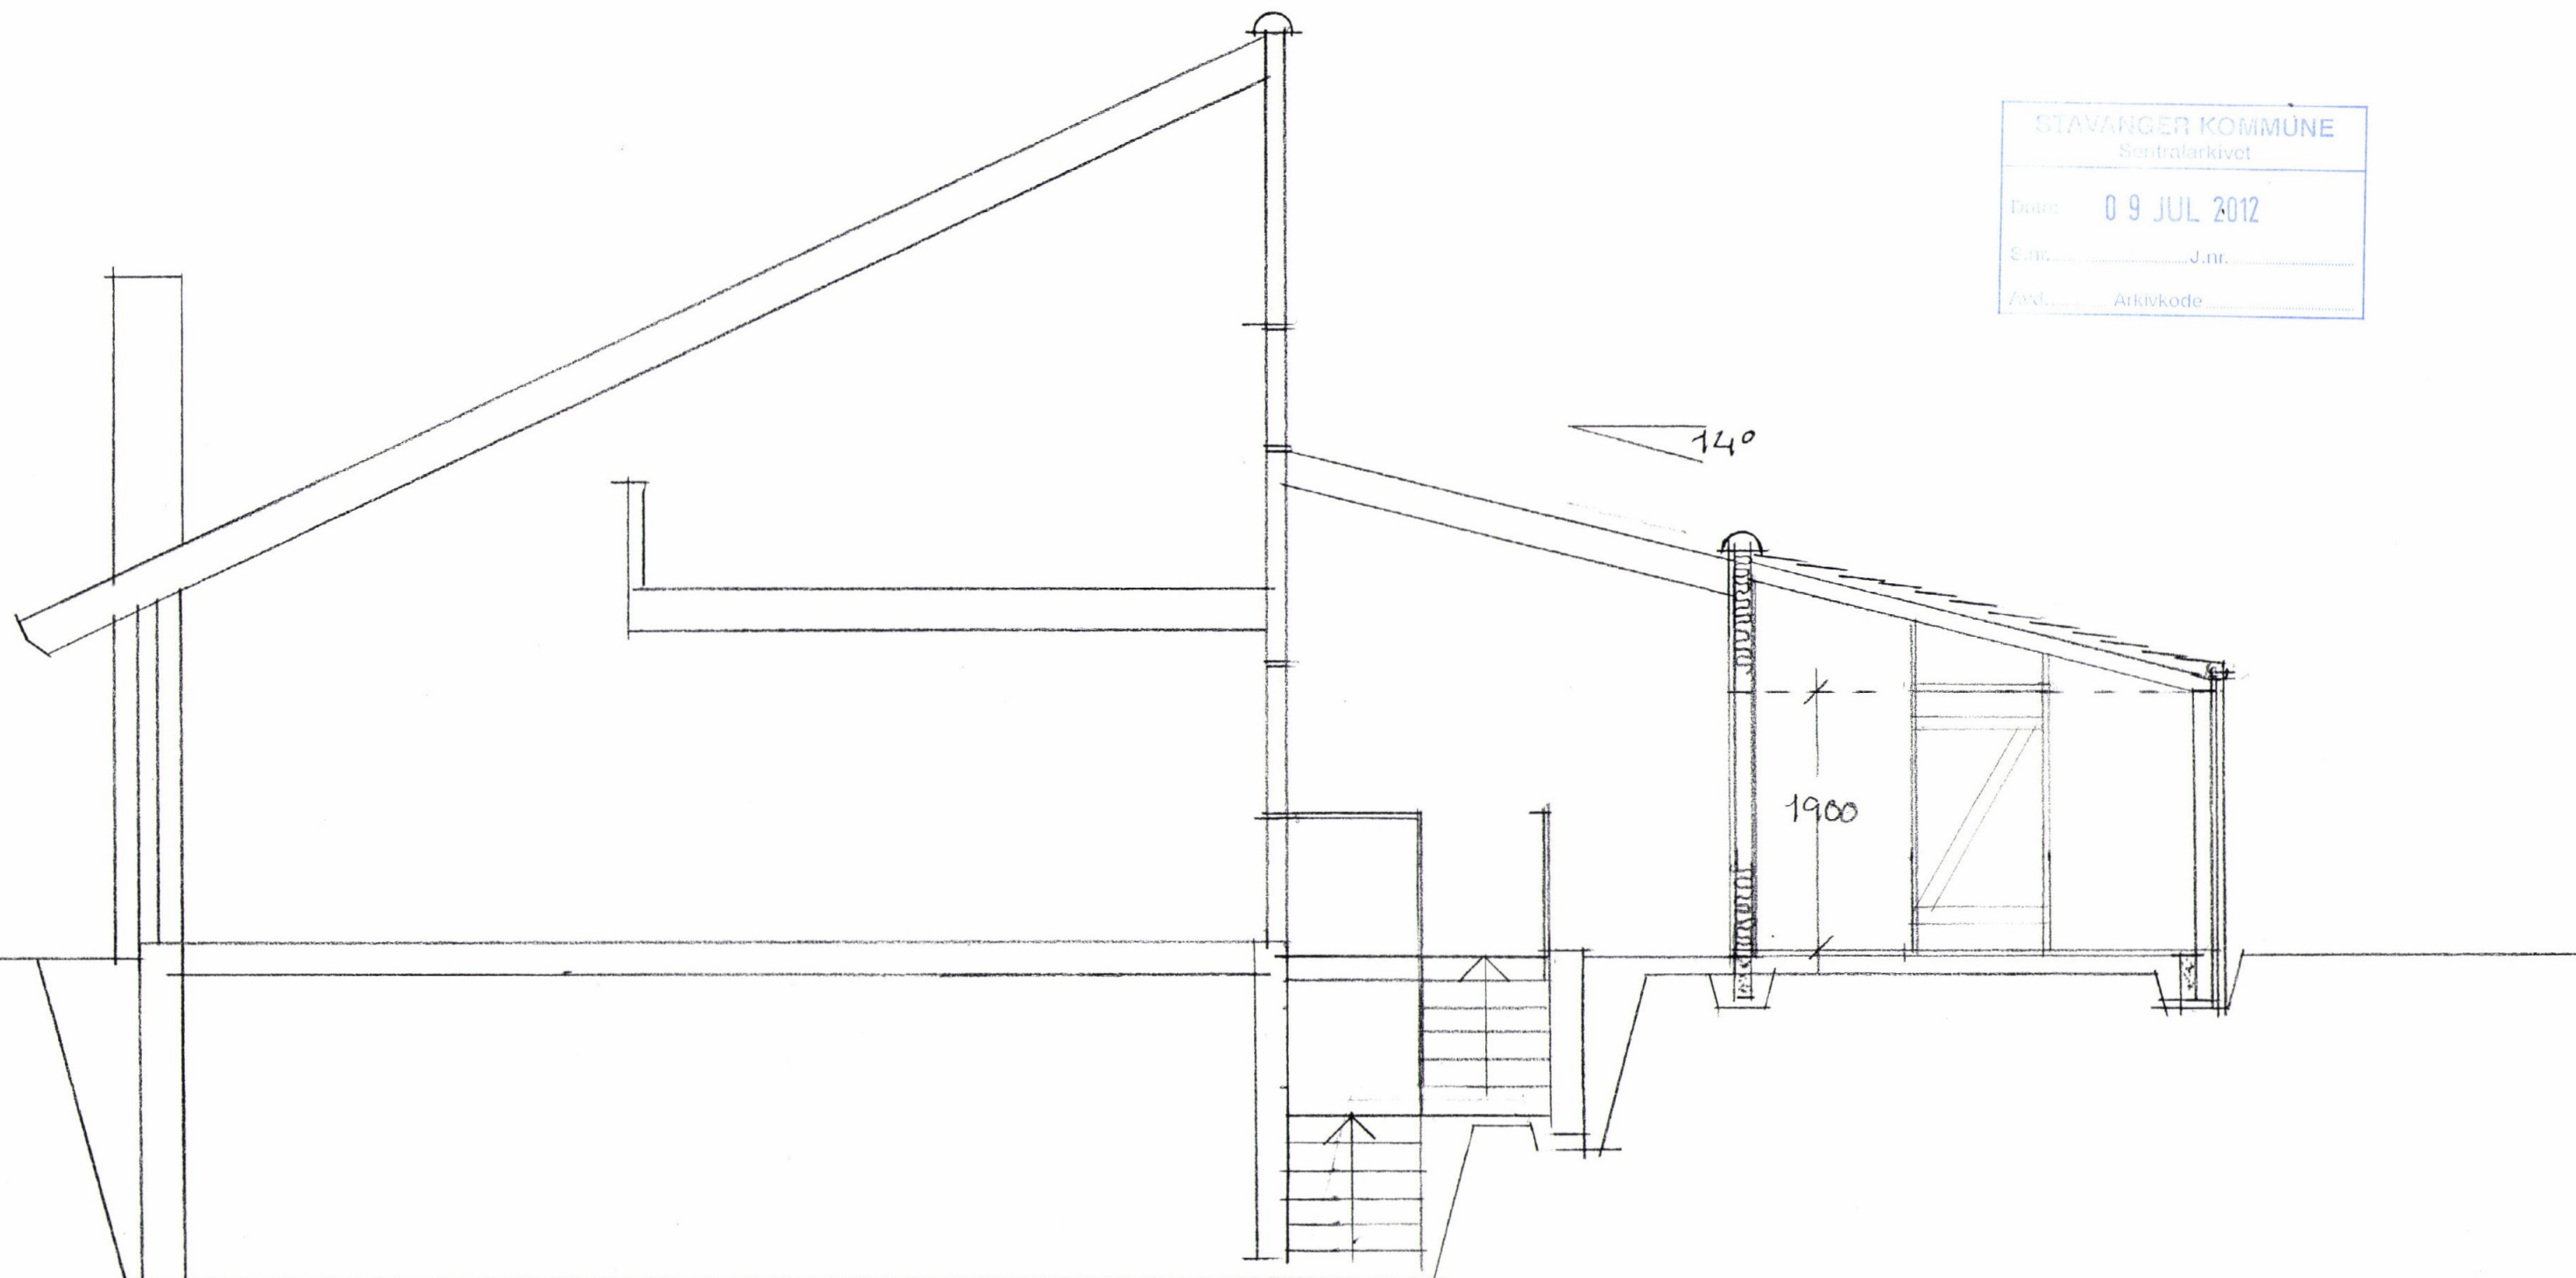


JAN PETERSENS GT OG ANTON BRØGGERS GT

SNITT AV BOD PÅ ADKOMSTSIDE MÅL 1:50


DATO 06-12-11 ARK THOR THOMASSEN

02

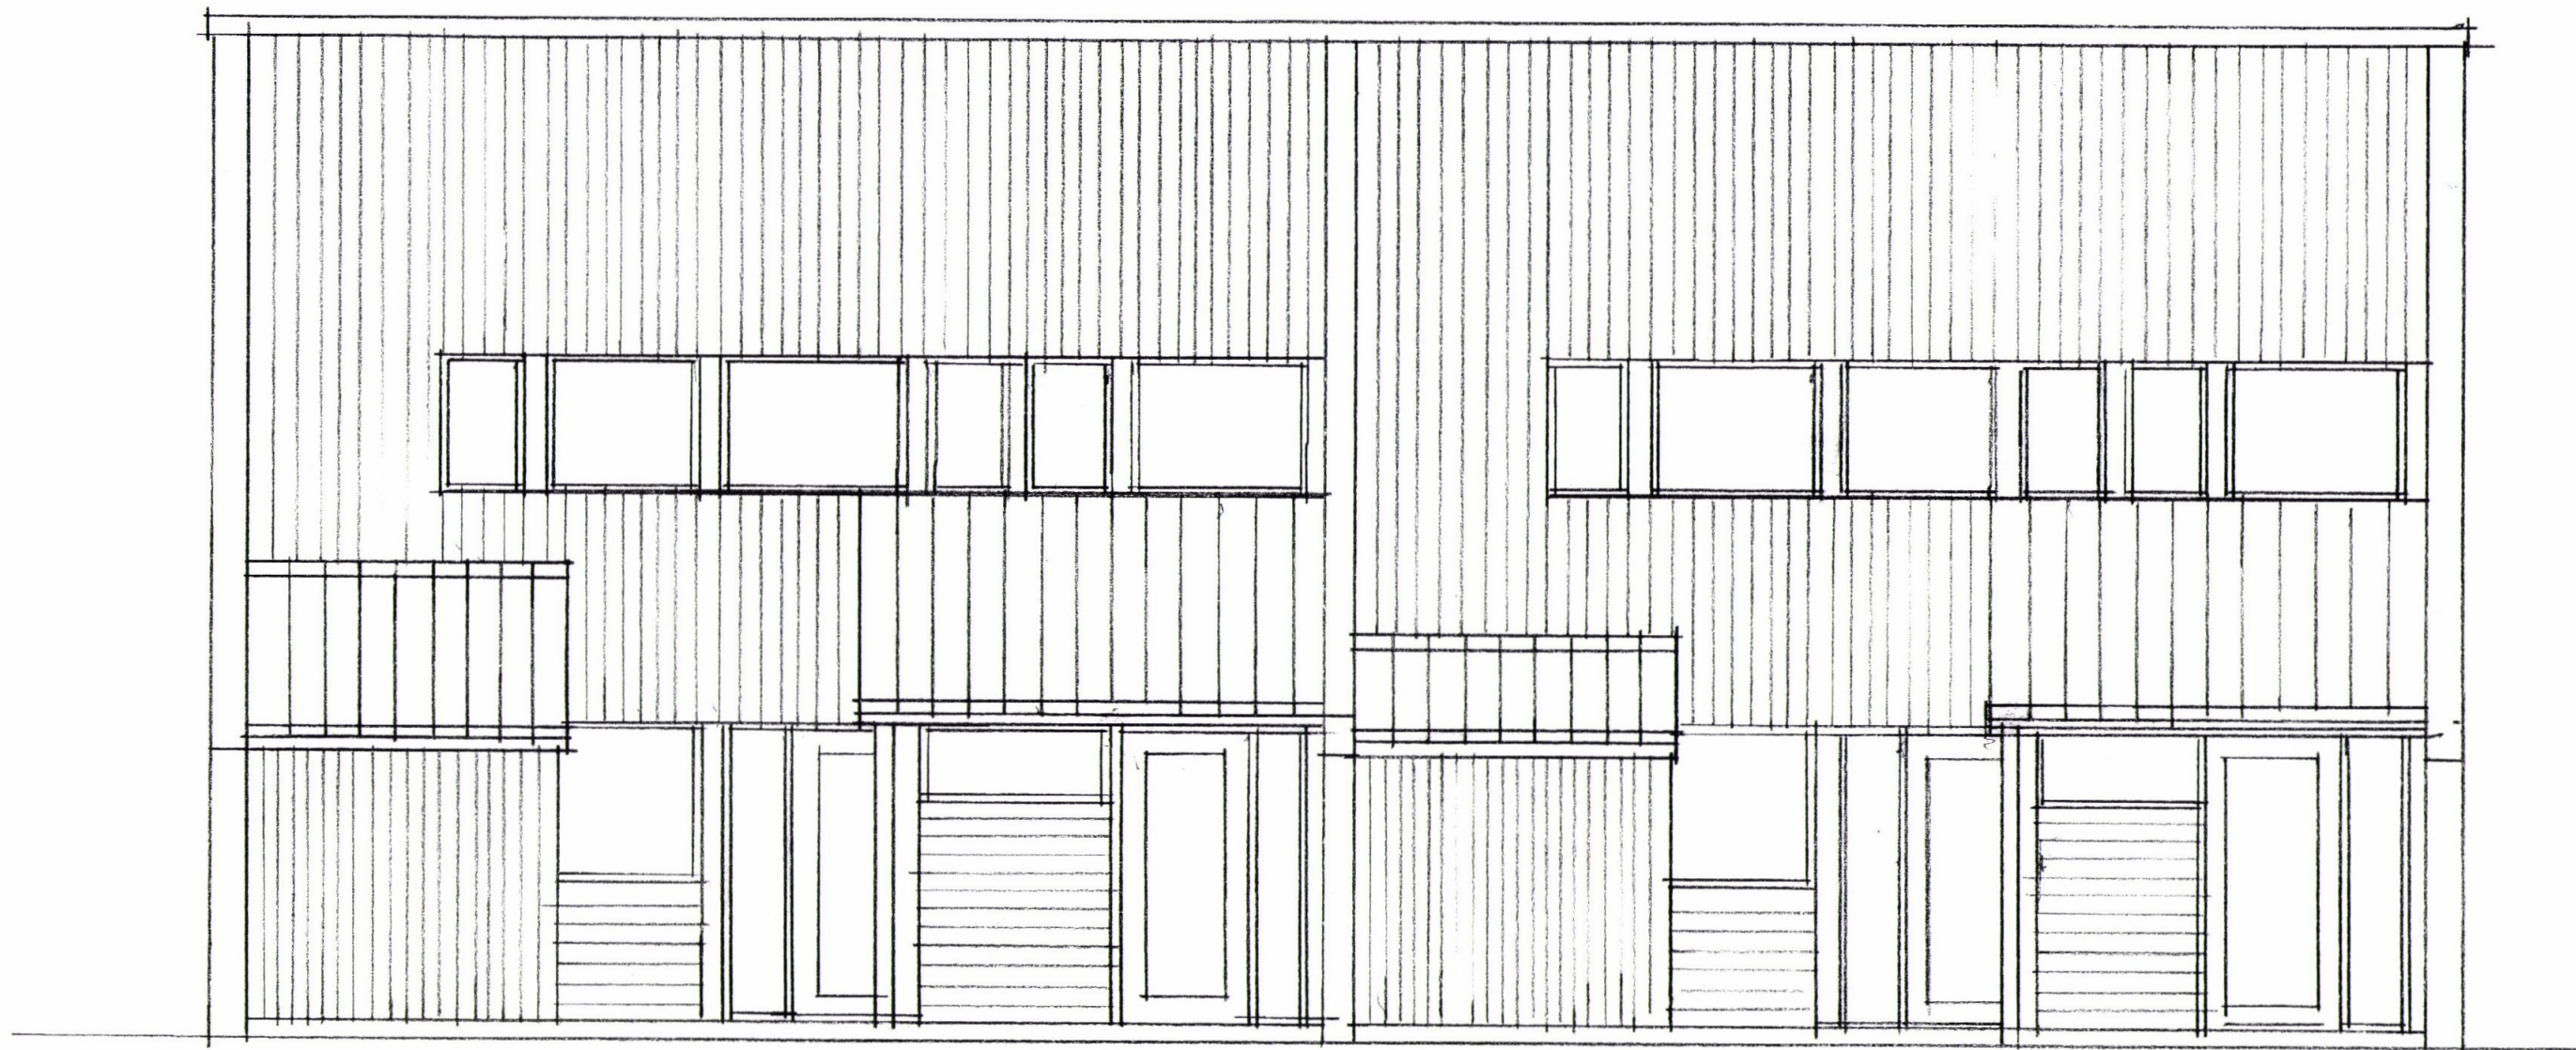


Arkivkode	Avd.
J.nr.	S.nr.
0 9 JUL 2012	Dato:
Sejlskive	STAVANGER KOMMUNE

JAN PETERSENS GT. OG ANTON BRØGGERSGT.
PASADE MOT ØST
DATO 02-01-12 MÅL 1:500 ARK THOR THOMASSEN

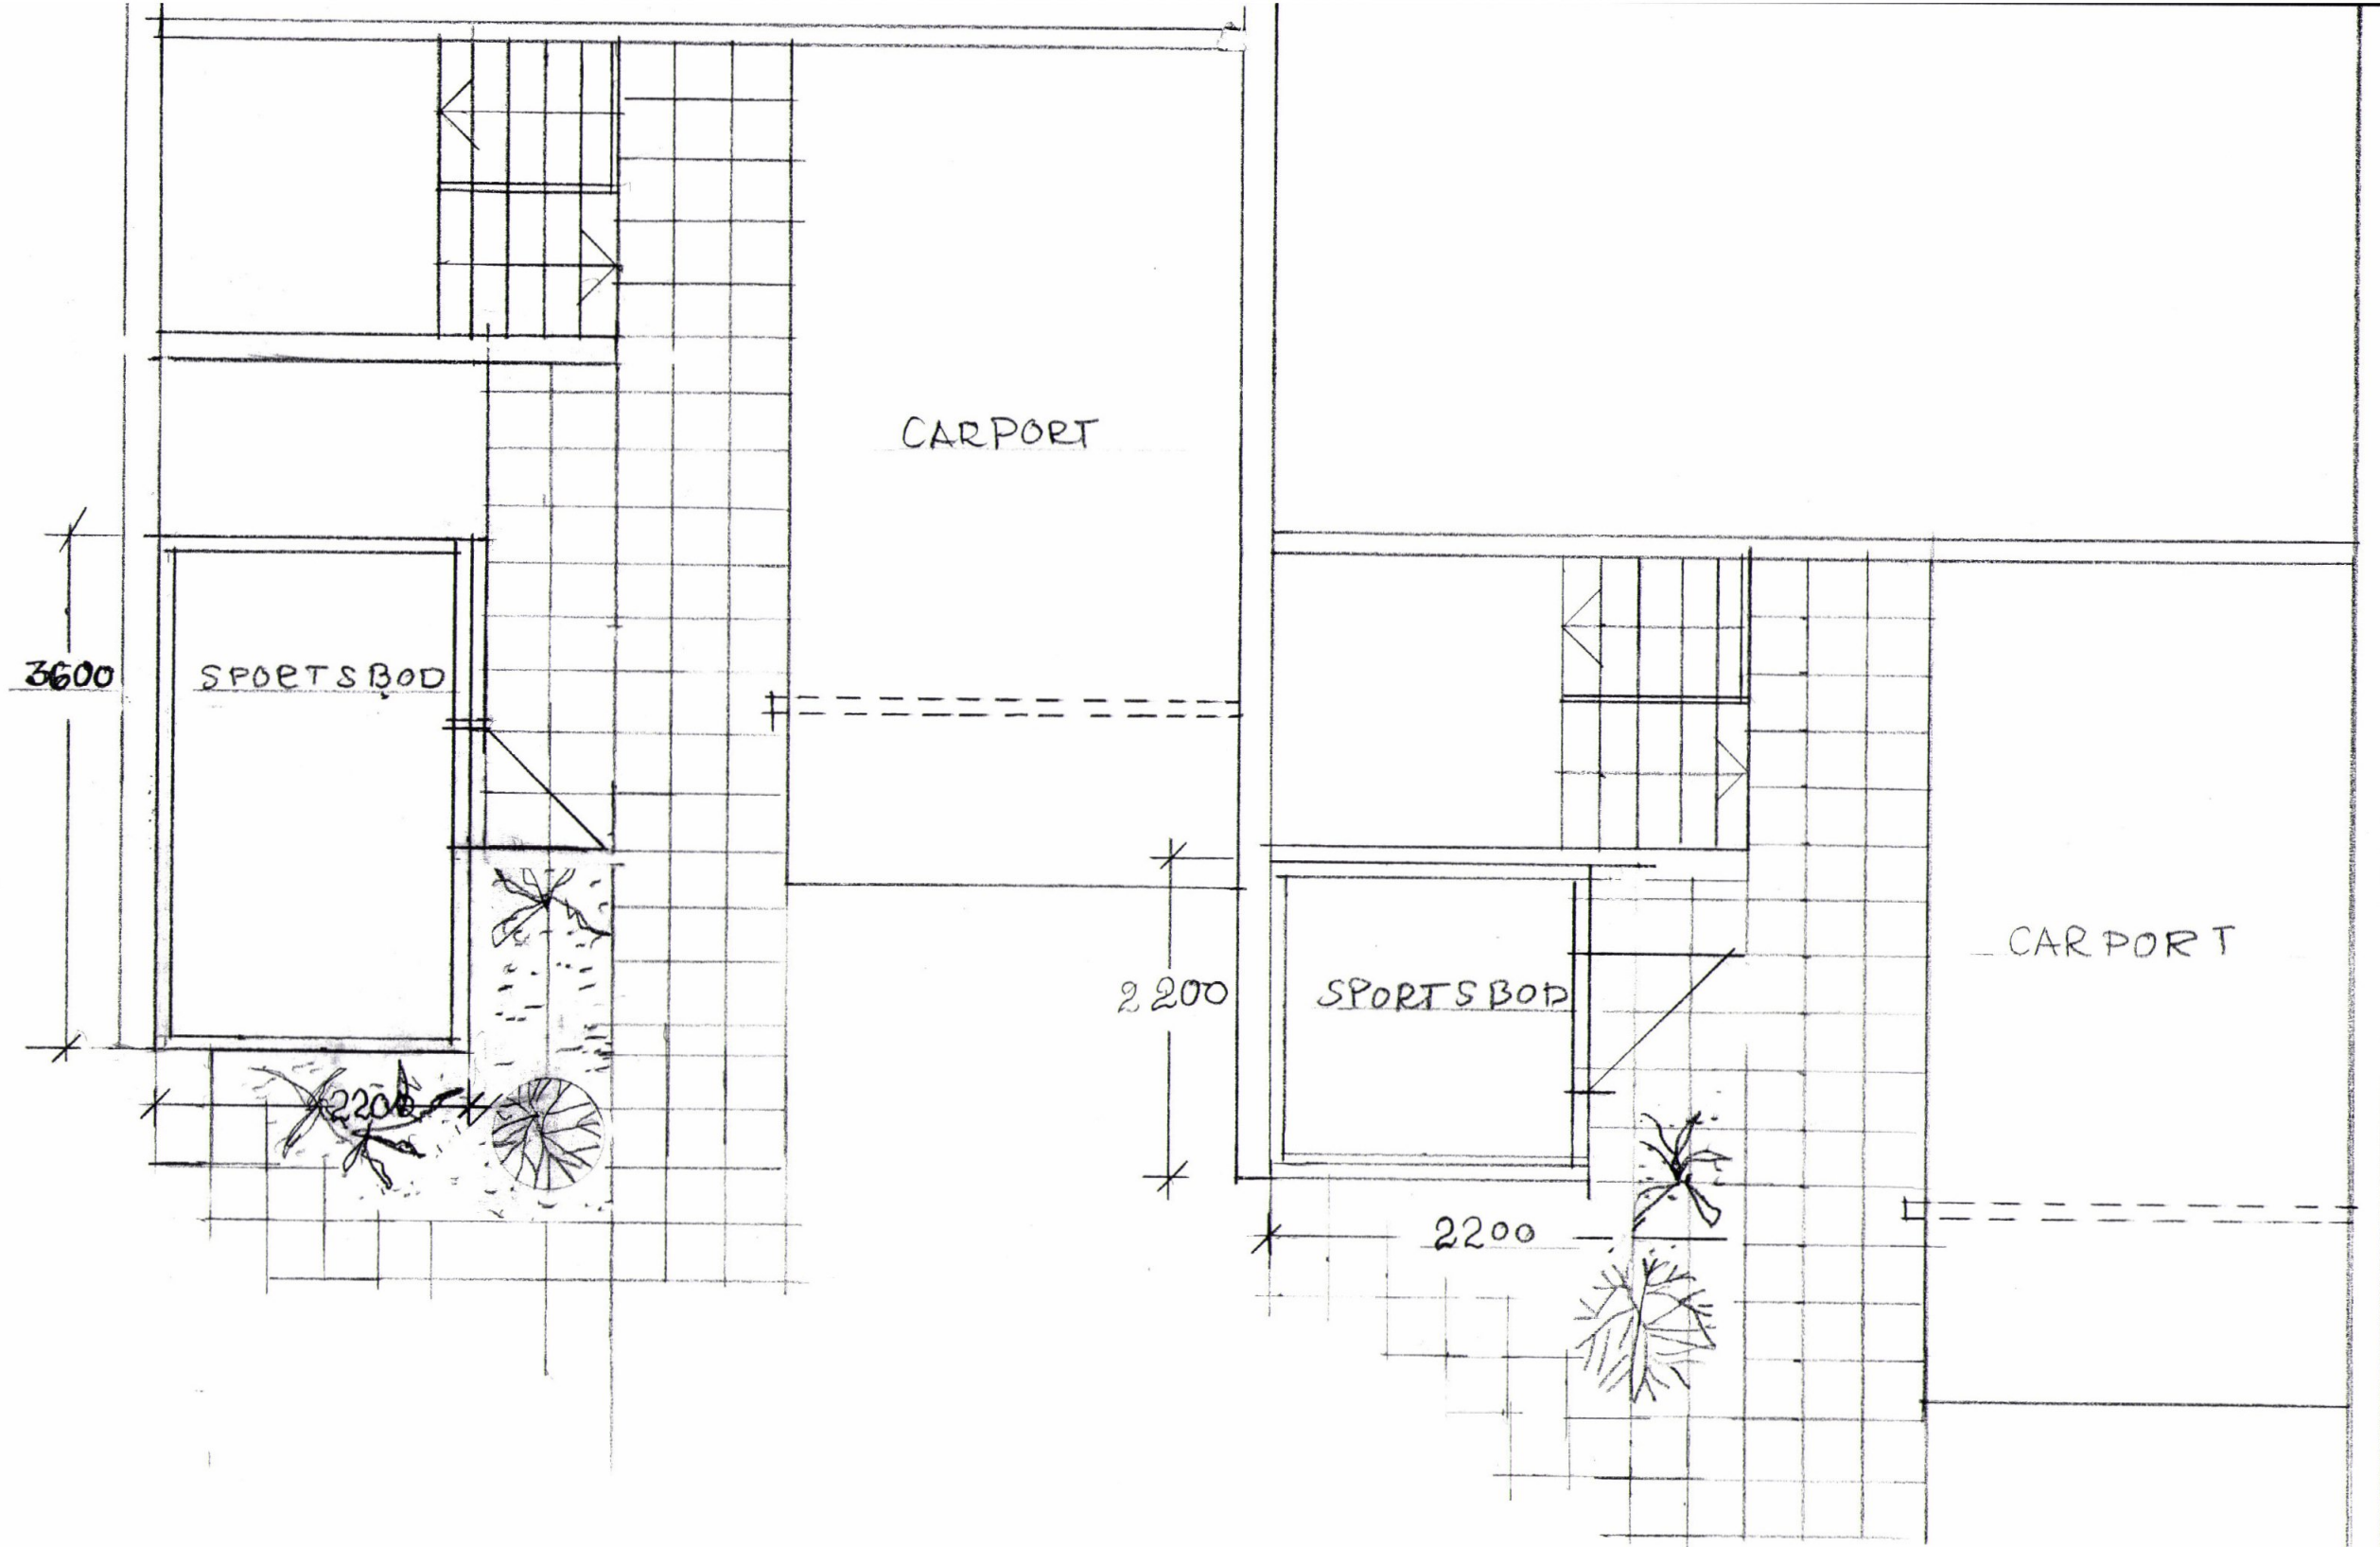


Avd.	Artikode
S.nr.	J.nr.
Dato: 09 JUL 2012	
STAVANGER KOMMUNE	
Sentralarkivet	

JAN PETERSENS GT OG ANTON BRØCCERES GT.
 PLANER FOR BOD PÅ ADKOMSTSIDE MÅL 1:50
 DATO 06-12-11 ARK. THOR THOMASSEN

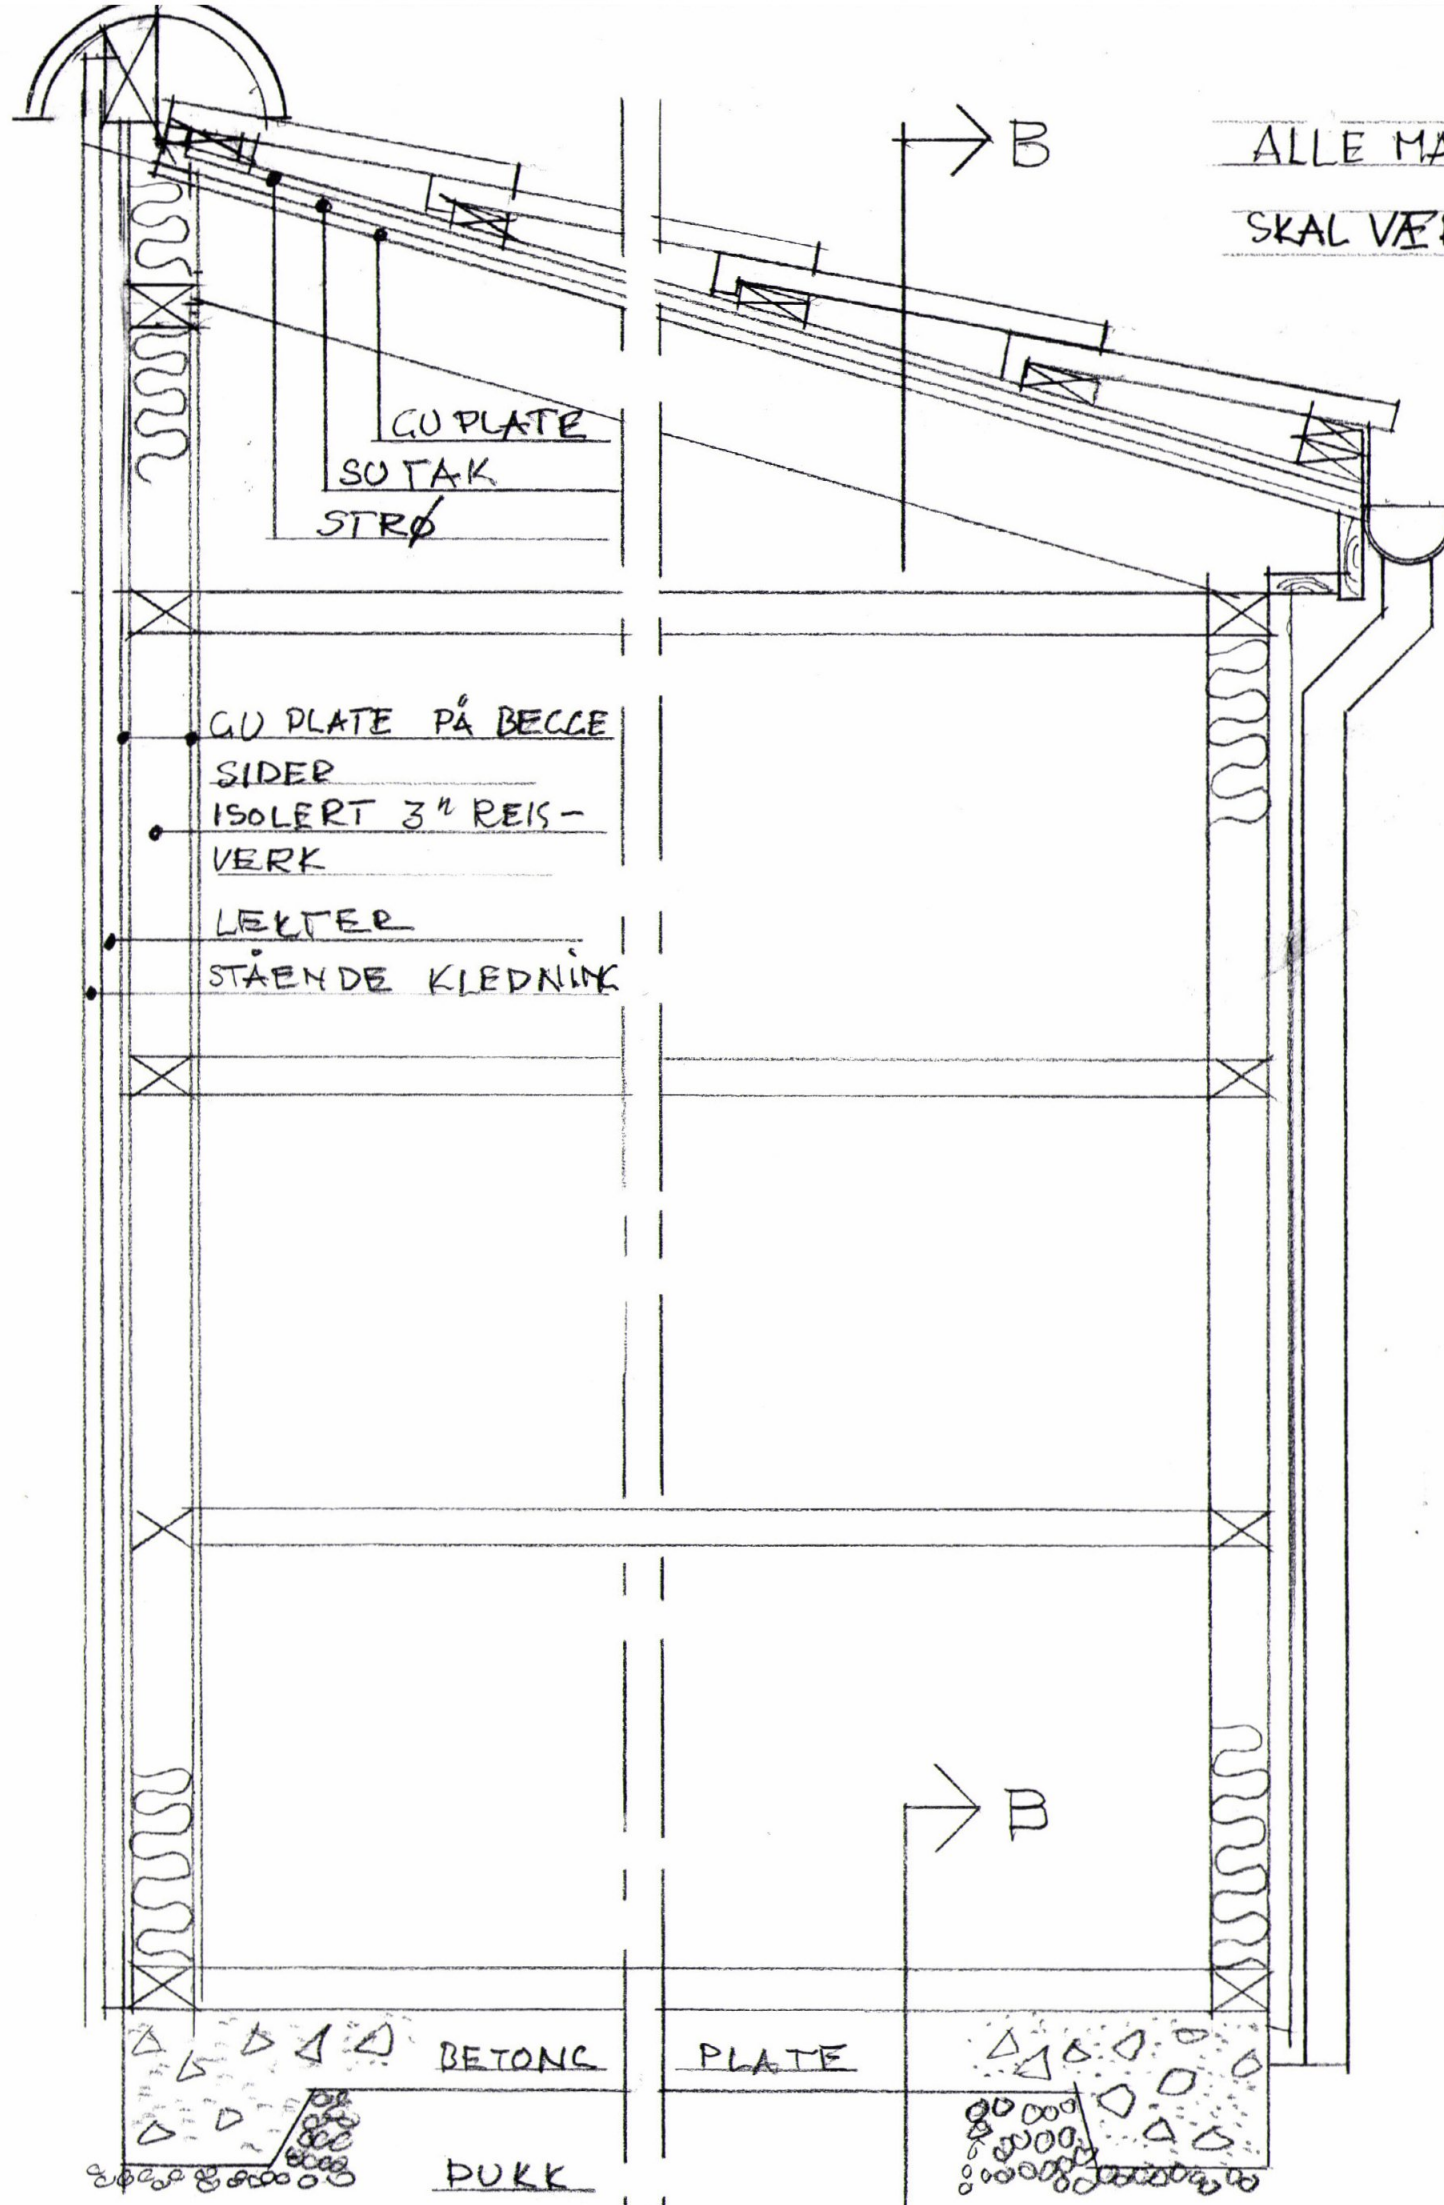

ALLE MATERIALER
SKAL VÆRE TRYKKIMP.

SNTT B-B

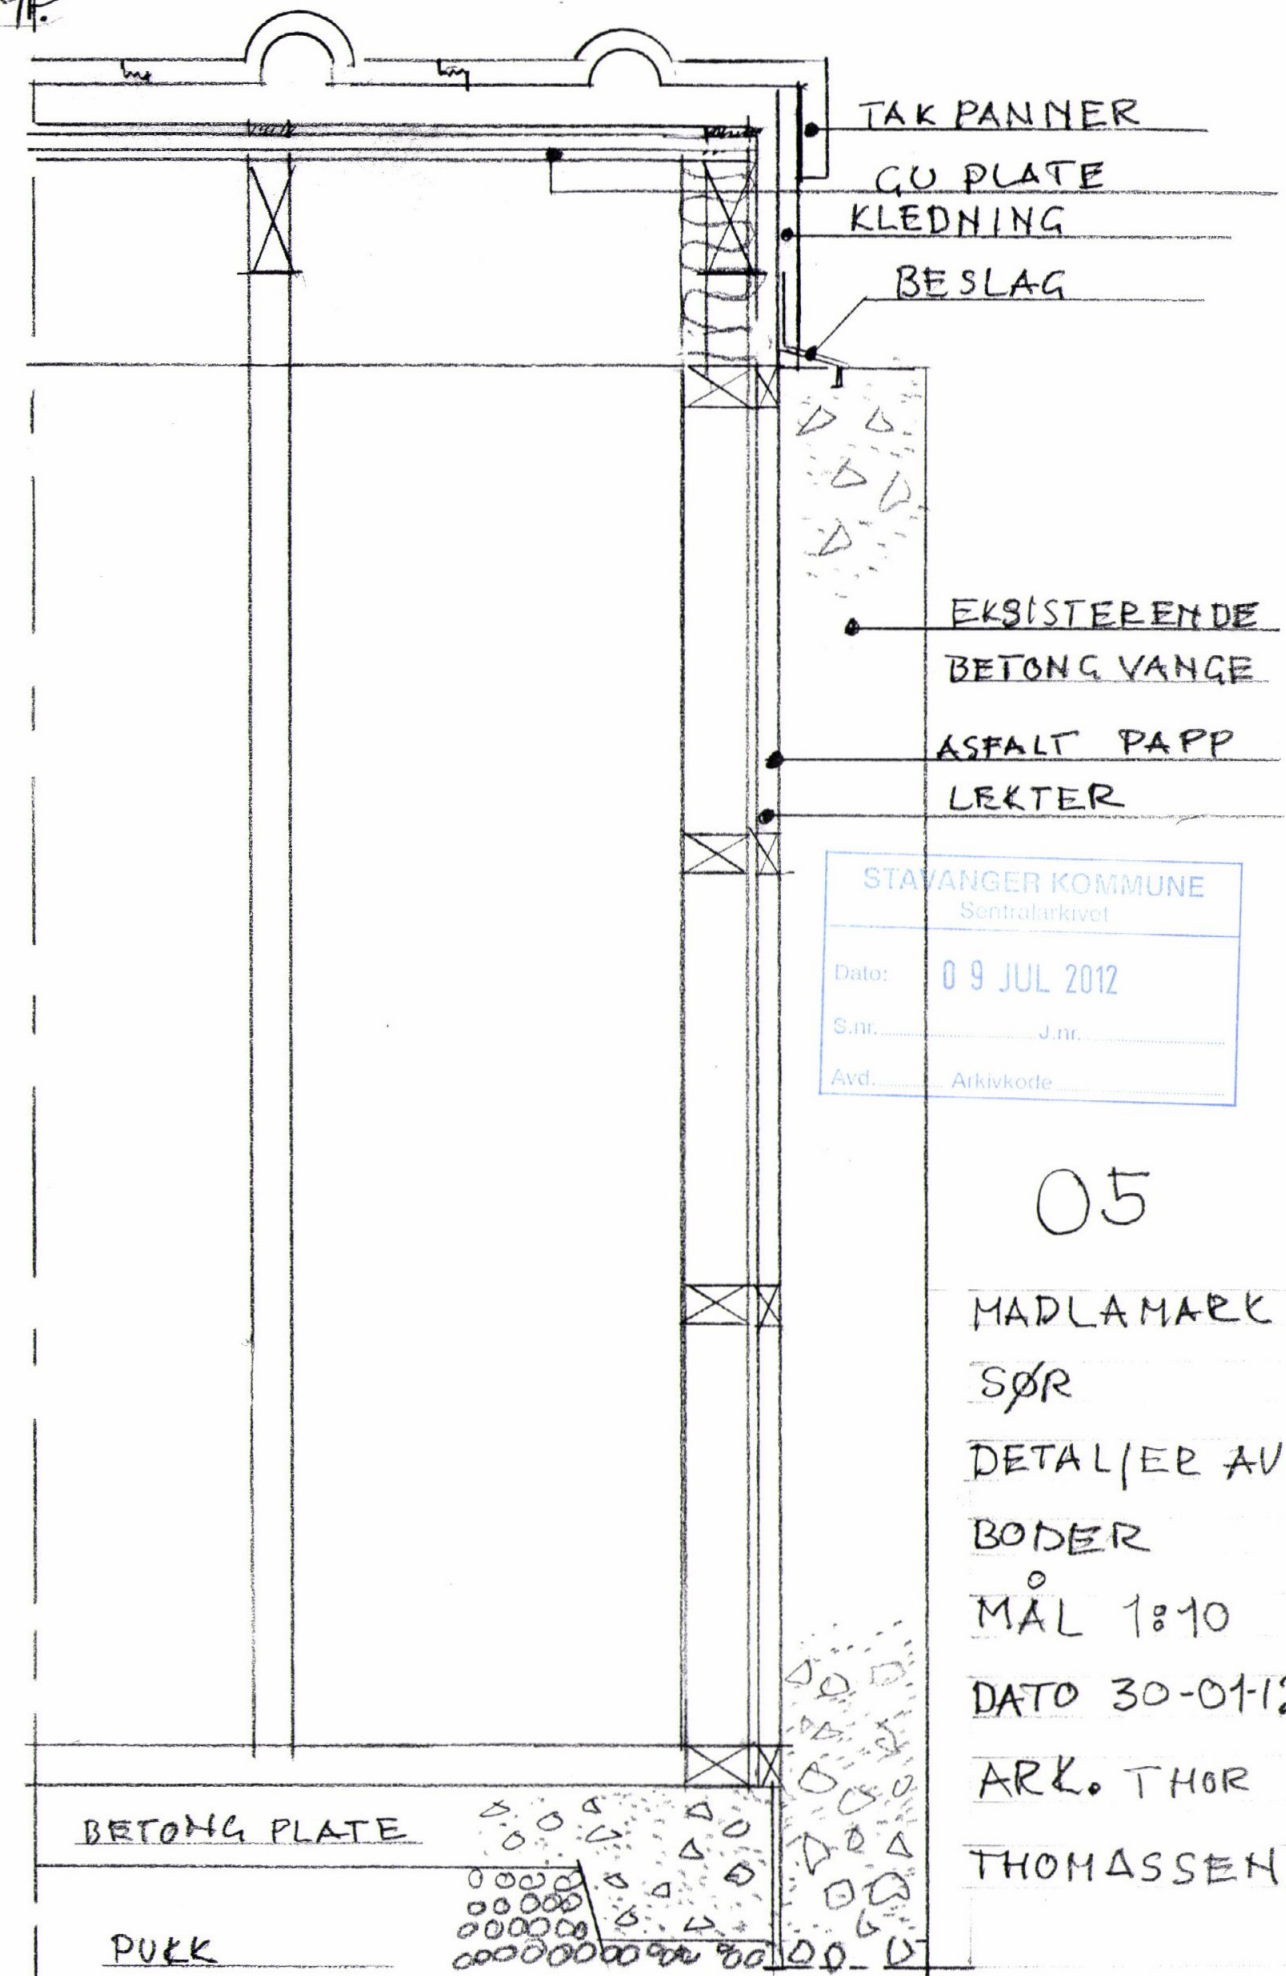

TAK PANNER
CU PLATE
KLEDNING
BESLAG

EKSISTERENDE
BETONG VANGE
ASFALT PAPP
LEKTER

STAVANGER KOMMUNE
Sentralarkivet
Dato: 09 JUL 2012
S.nr. J.nr.
Avd. Arkivkode

05

MADLAMARK
SØR
DETALJER AV
BODER
MÅL 1:10
DATO 30-01-12
ARK. THOR
THOMASSEN

BETONG PLATE

PUKK