


Stavanger Kommune
BYGNINGSSETATENE
26 SEP 1969



Arkiv nr. 503.1 J. nr. 3061

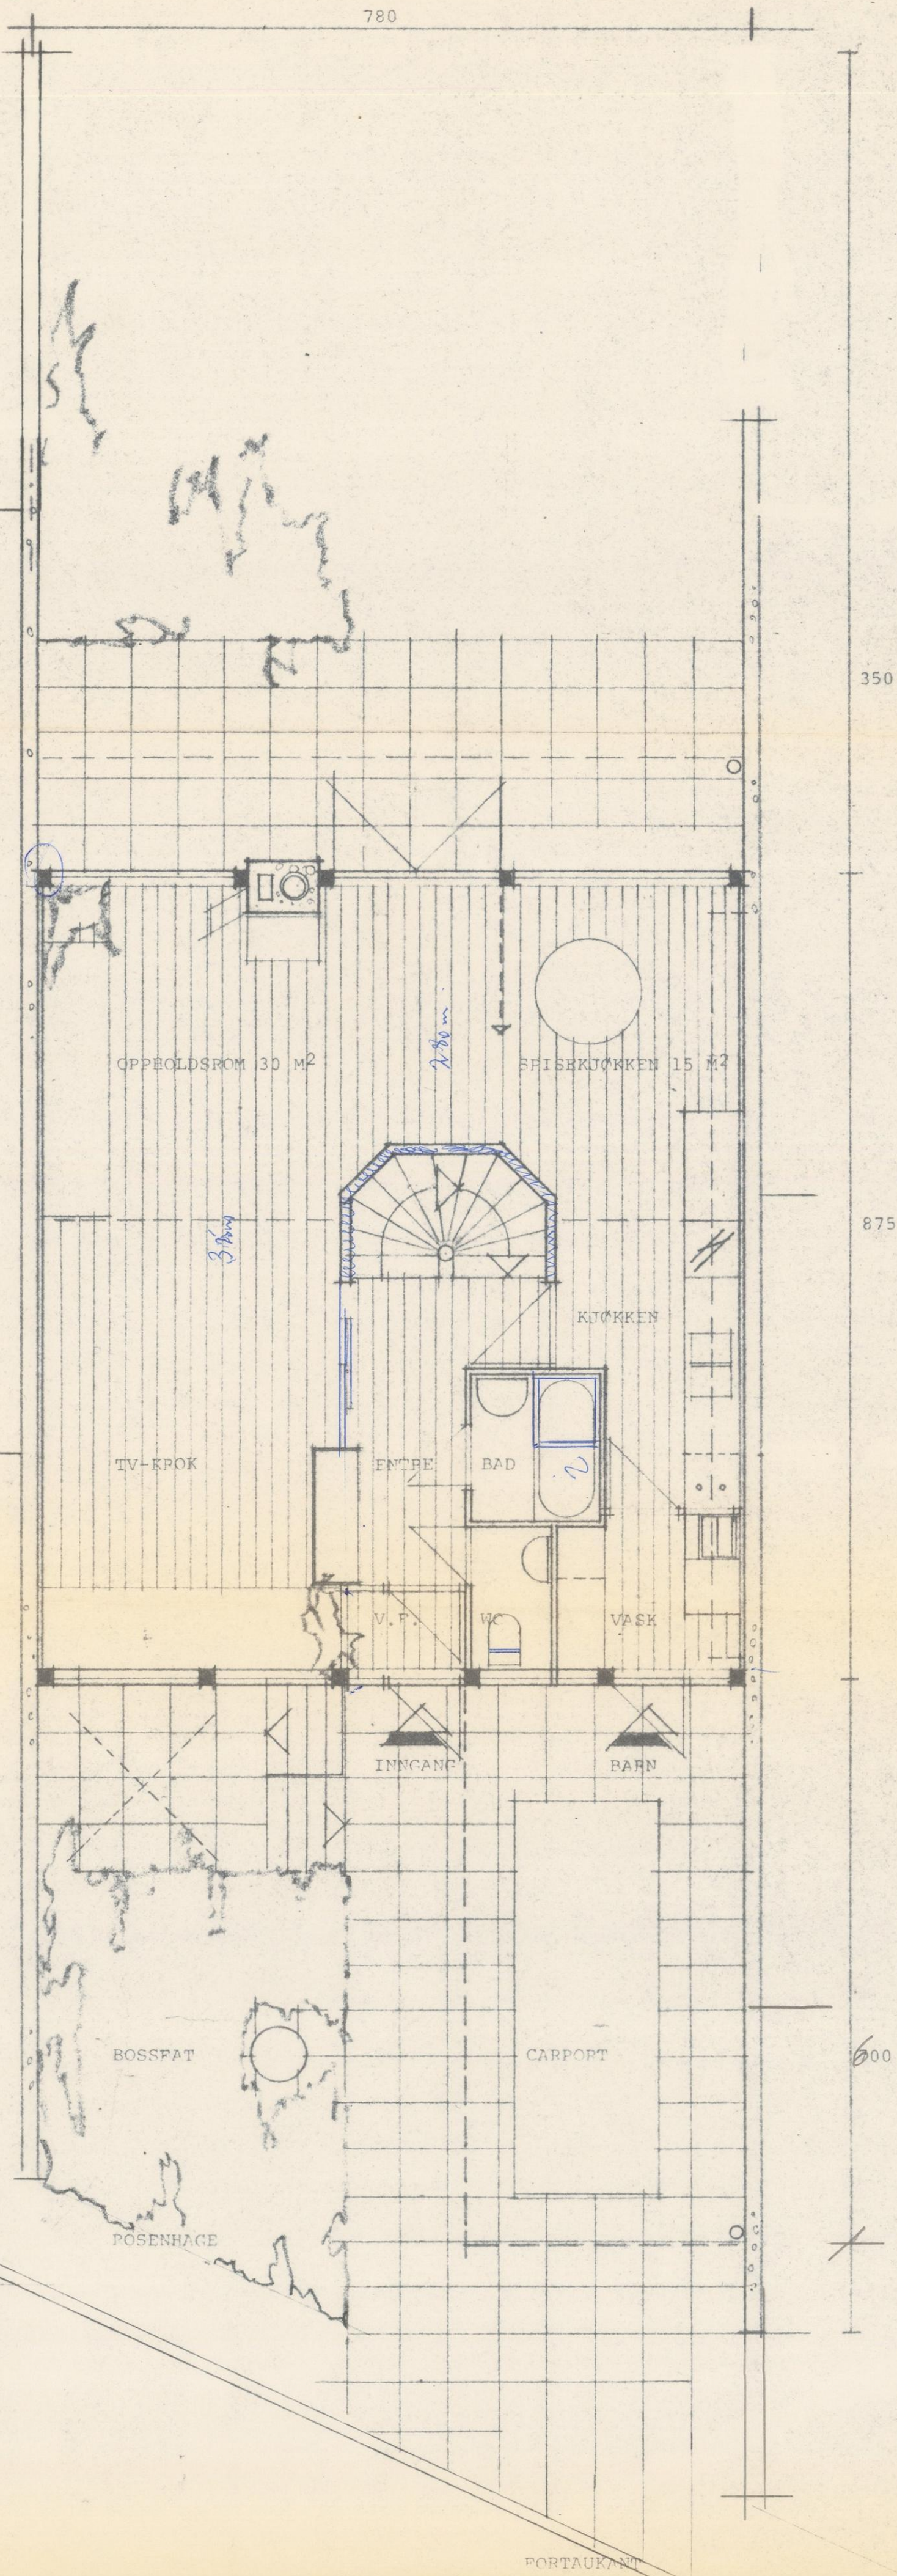


UGYLDIG
Erstattes av tegning datert:

Se plan 1. etasje - j.nr. 3929

102 BOLLIG-BYGG MADLAMARKA-SØR
AIDV PLAN 1. ETASJE MAL 1:50

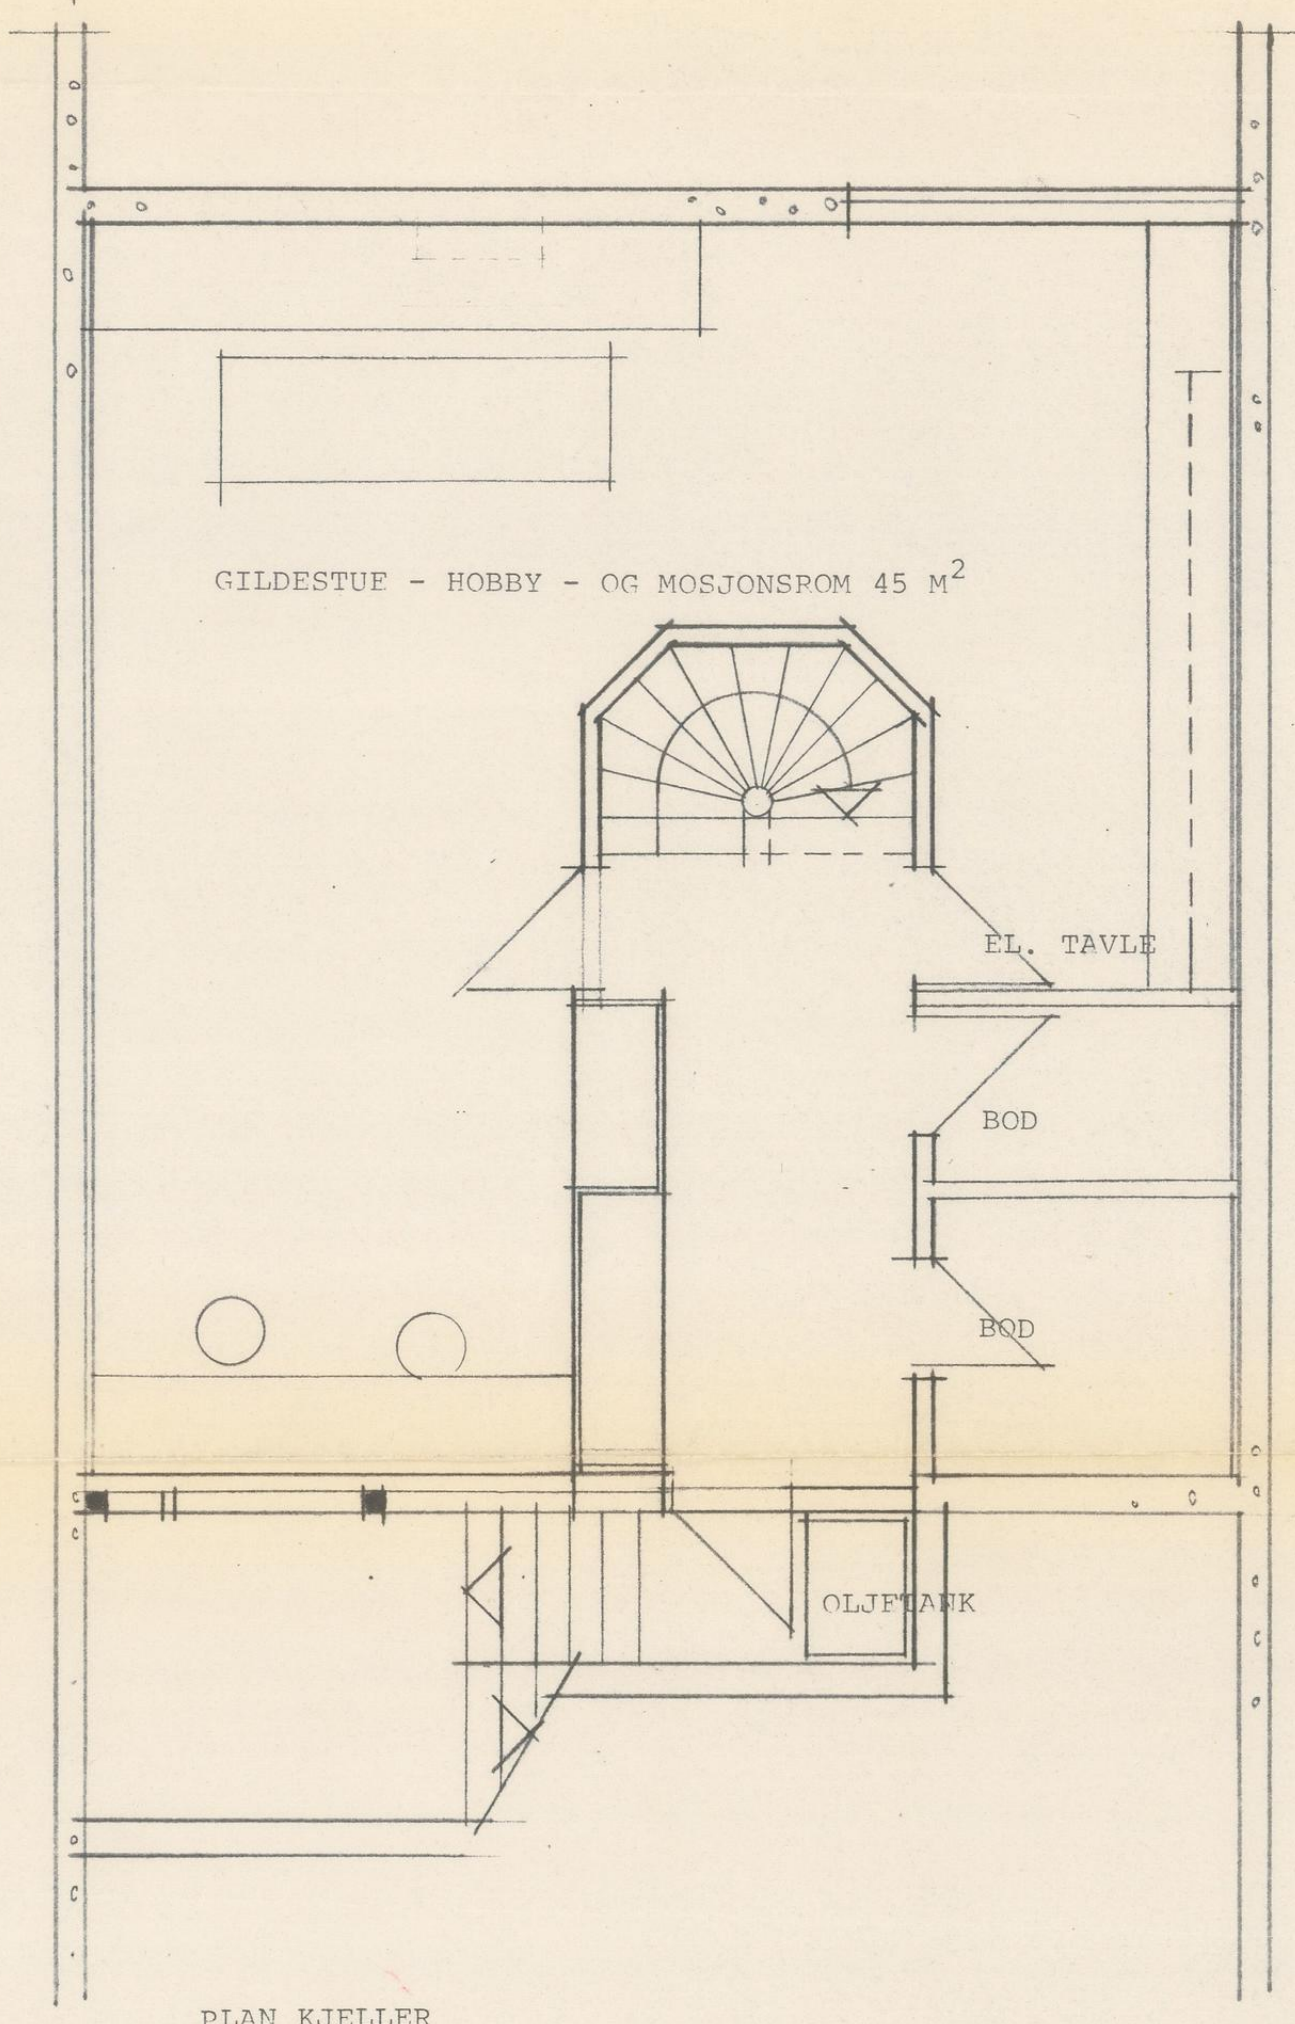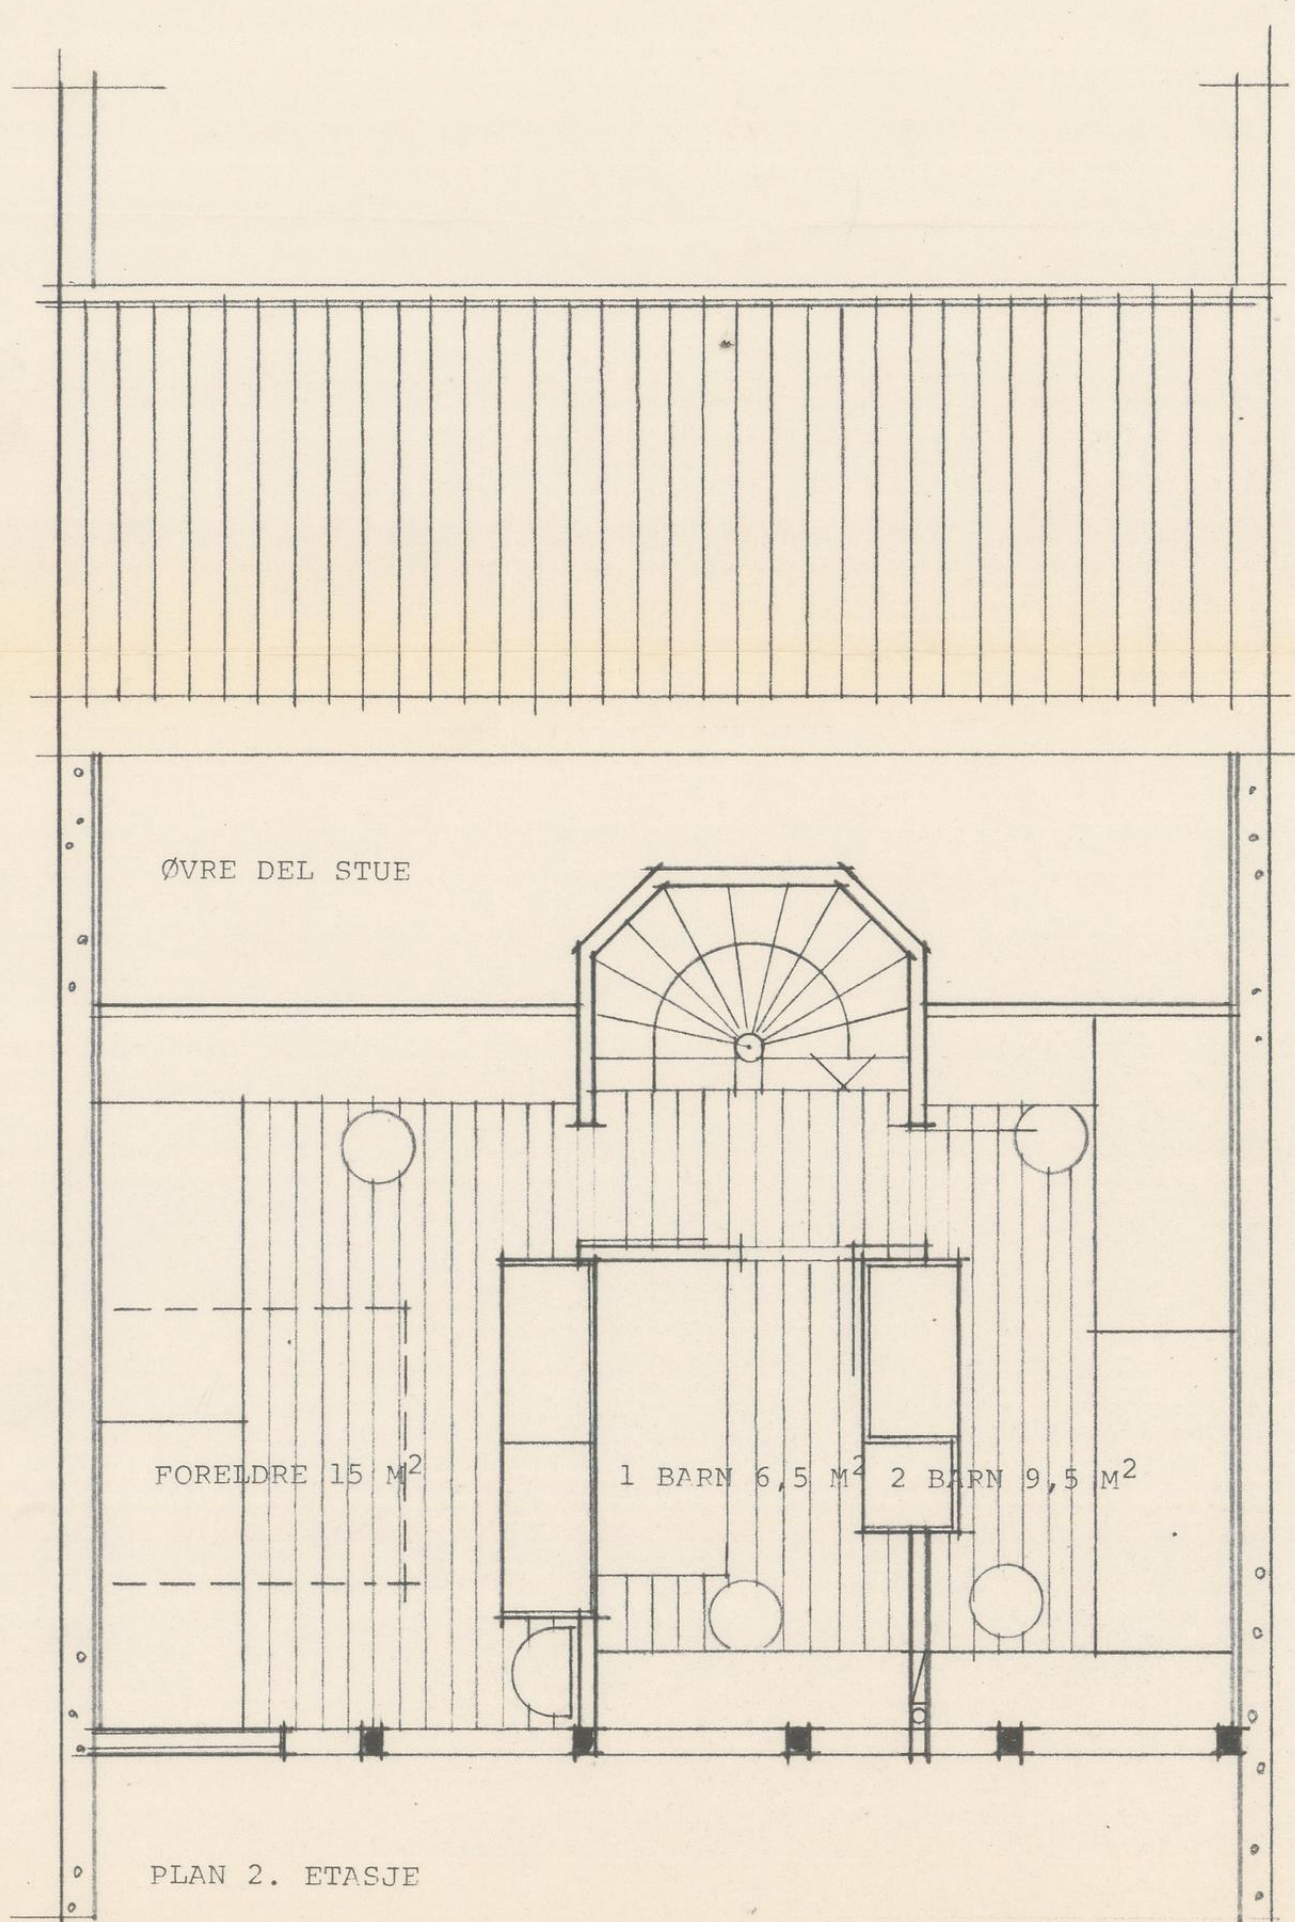

UGYLDIG
Erstattet av tegning datert:

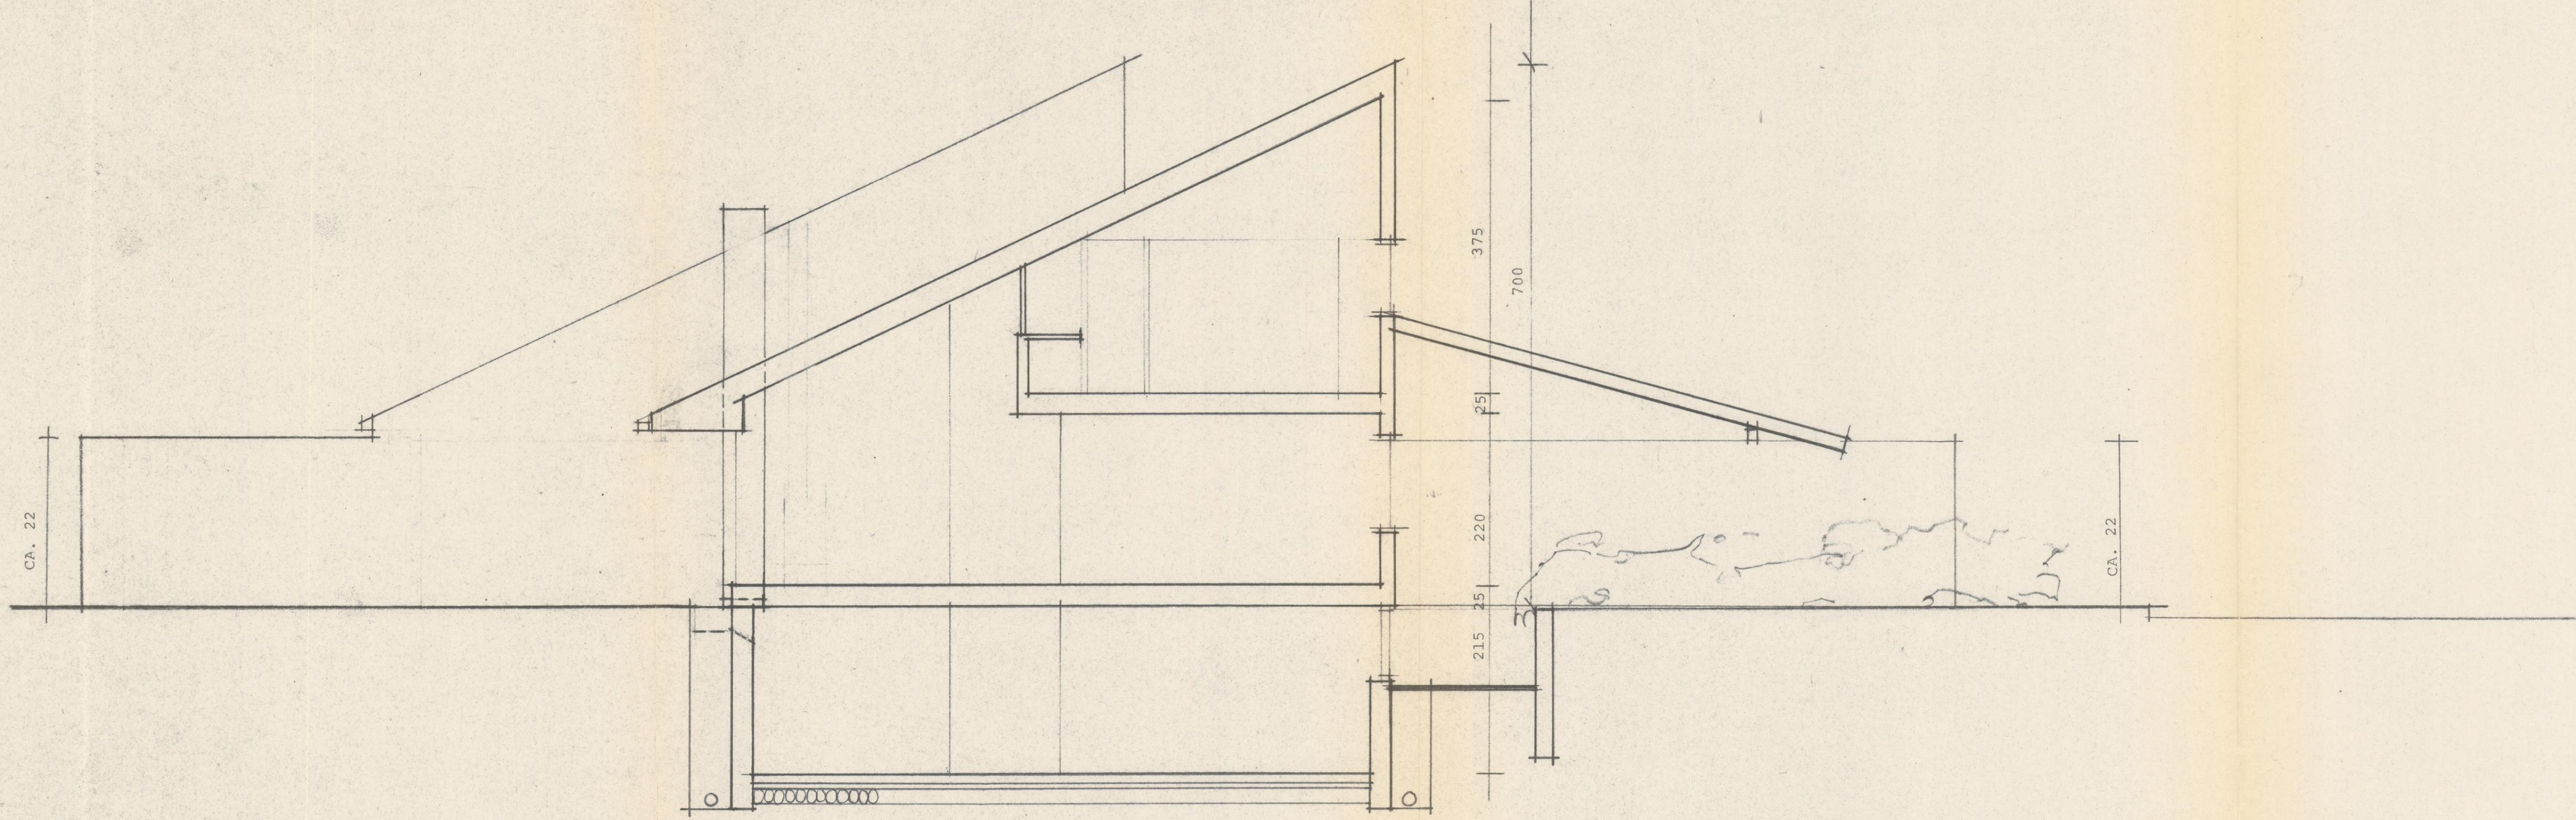

Stavanger Kommune
BYGN. S. AENE
2. 1589

Arkiv nr. 1 3061


UGYLDIG
Erstatning for tegning detert:

102
A12

BOLIG-BYGG
SNITT

MADLAMARIKASØR
MÅL 1:50


INGEBORG OG KNUT HOEM ARKITEKTER MNAL STVGR. AUG. 1969

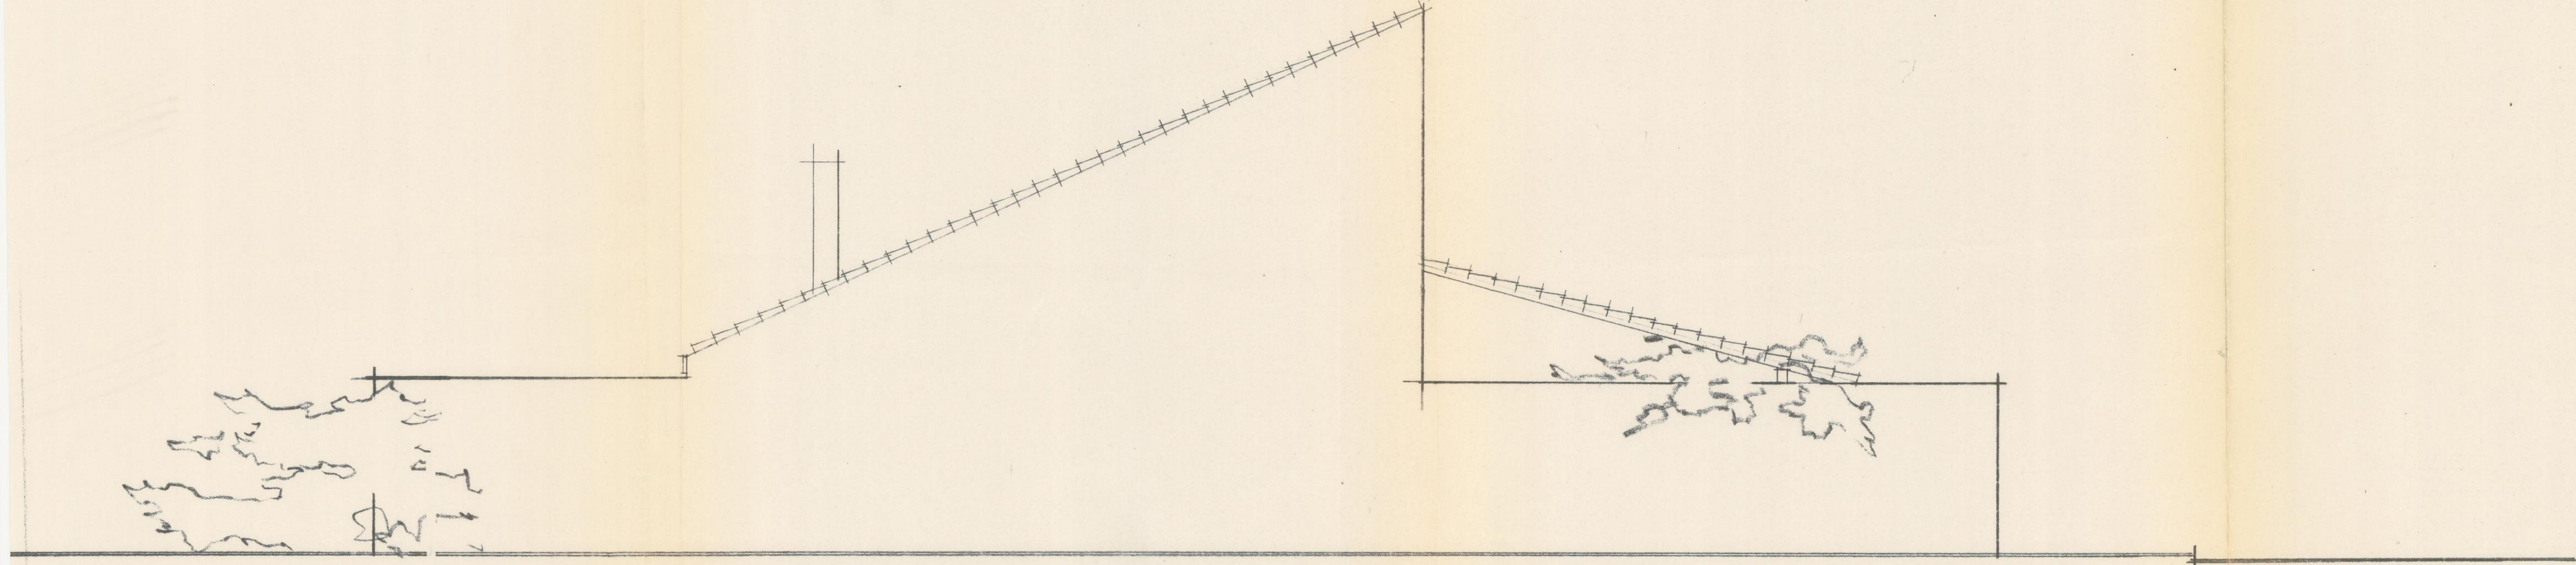


Stavanger Kommune
BYGNINGSSETAENE
26 SEP 1969
J. nr. 3061
Arkiv nr. 5021

~~UGYLDIG~~
Erstattet av tegning datert:

102 BOLLIG-BYGG MADDAMARIKA-SØR
A163 FASADDE MAIL 1:500

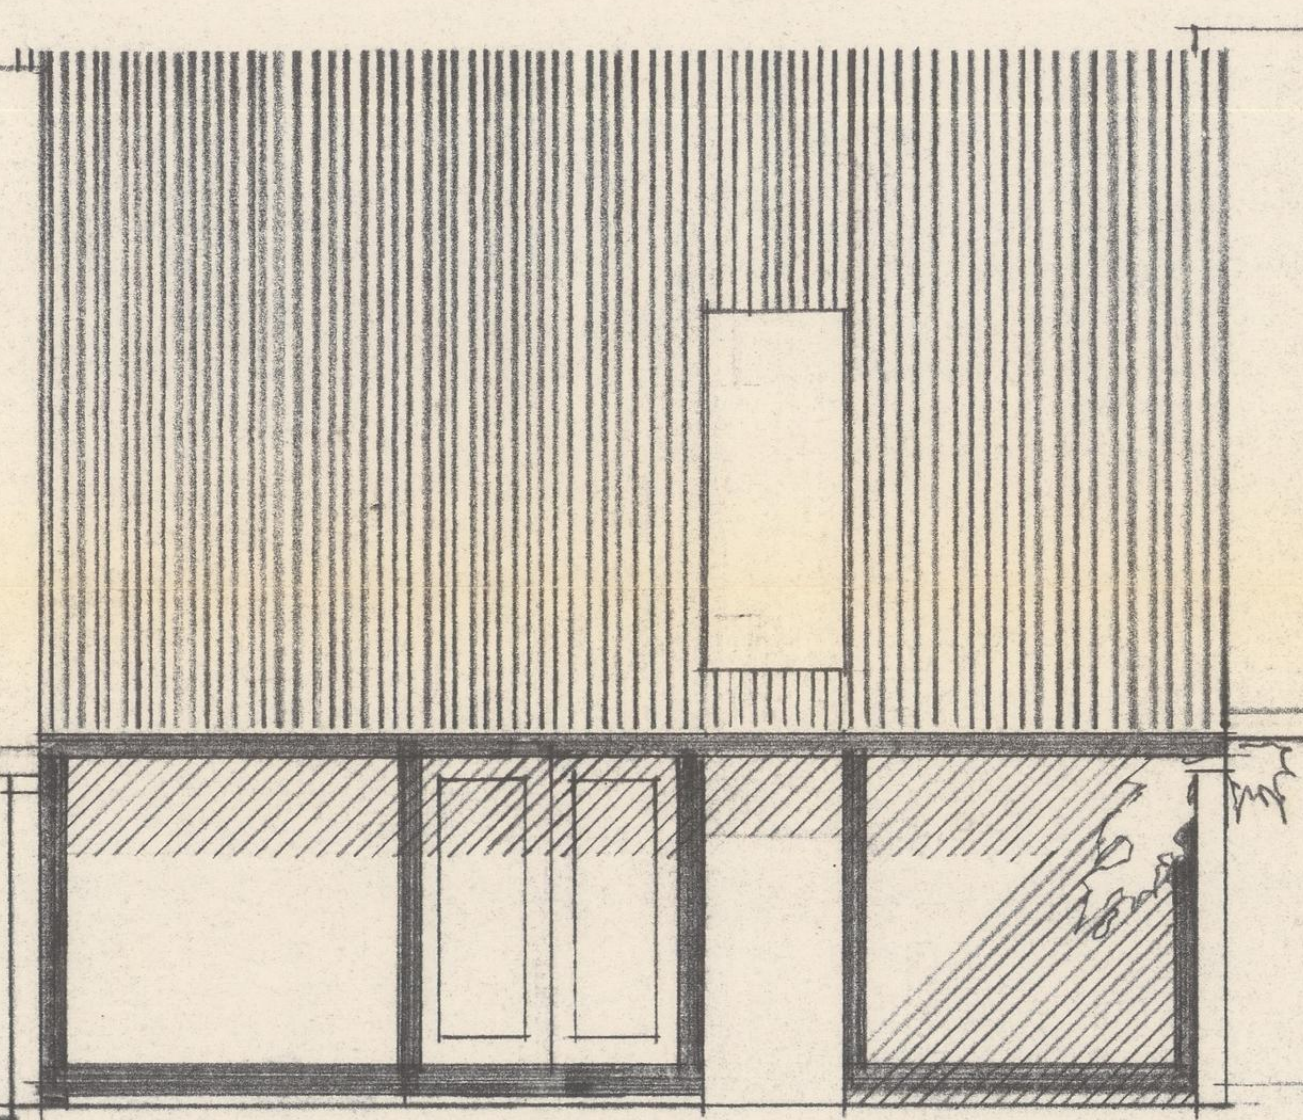

MOT SYDVEST

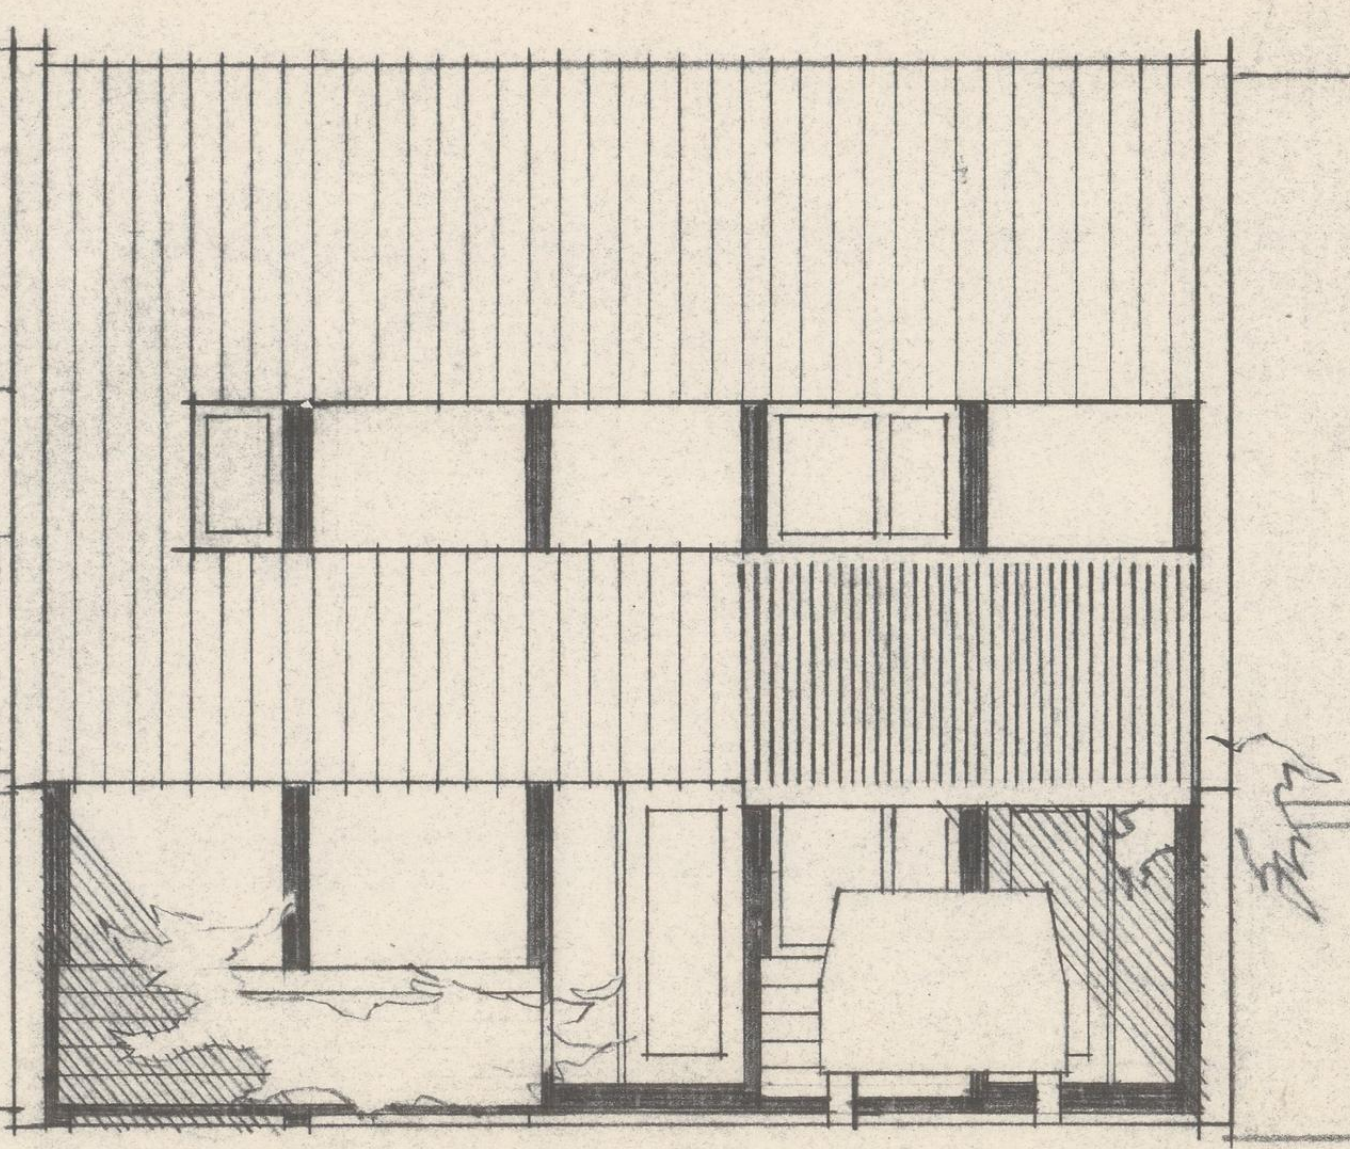


MOT NORDØST


~~UGYLDIG~~
Erstattet av tegning datert:

Stavanger Kommune
BYGGSAKSBEHANDLING
2. juni 1969
Arkiv nr. 1001 3061


102 BOLLIG-BYGG MAIDLAMARKA-SØR
A14 FASADDER MÅL 1:50

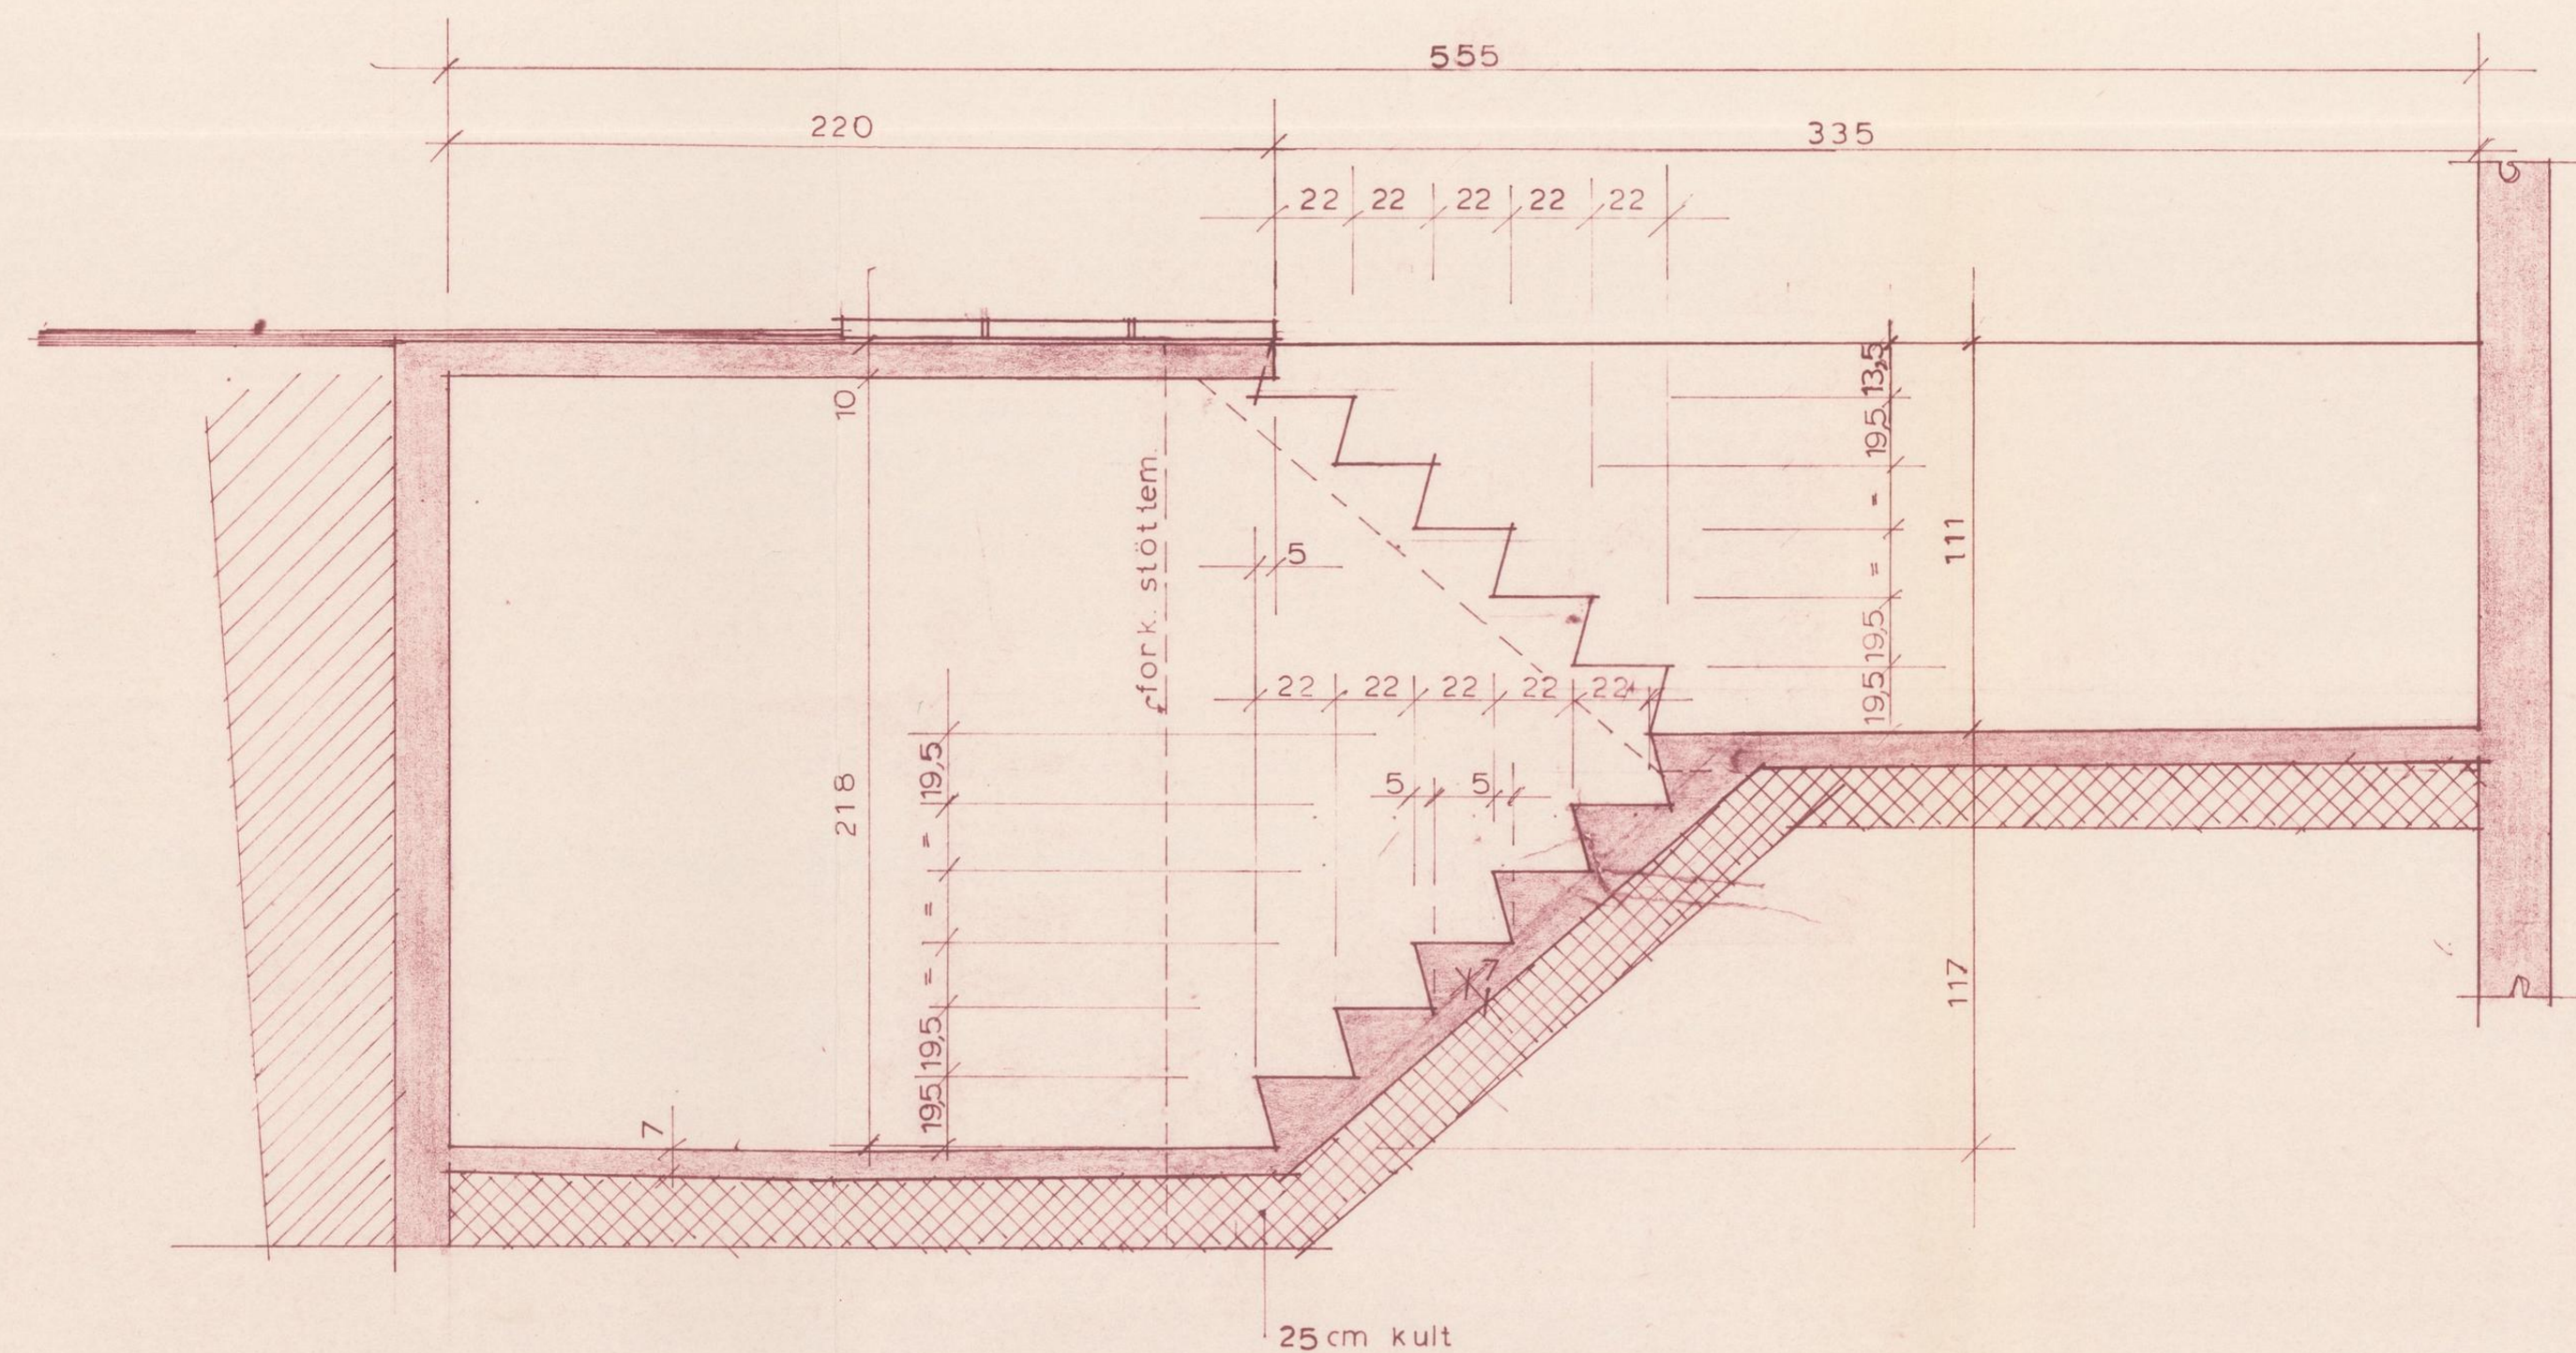

SNITT 5-5 M 1:20

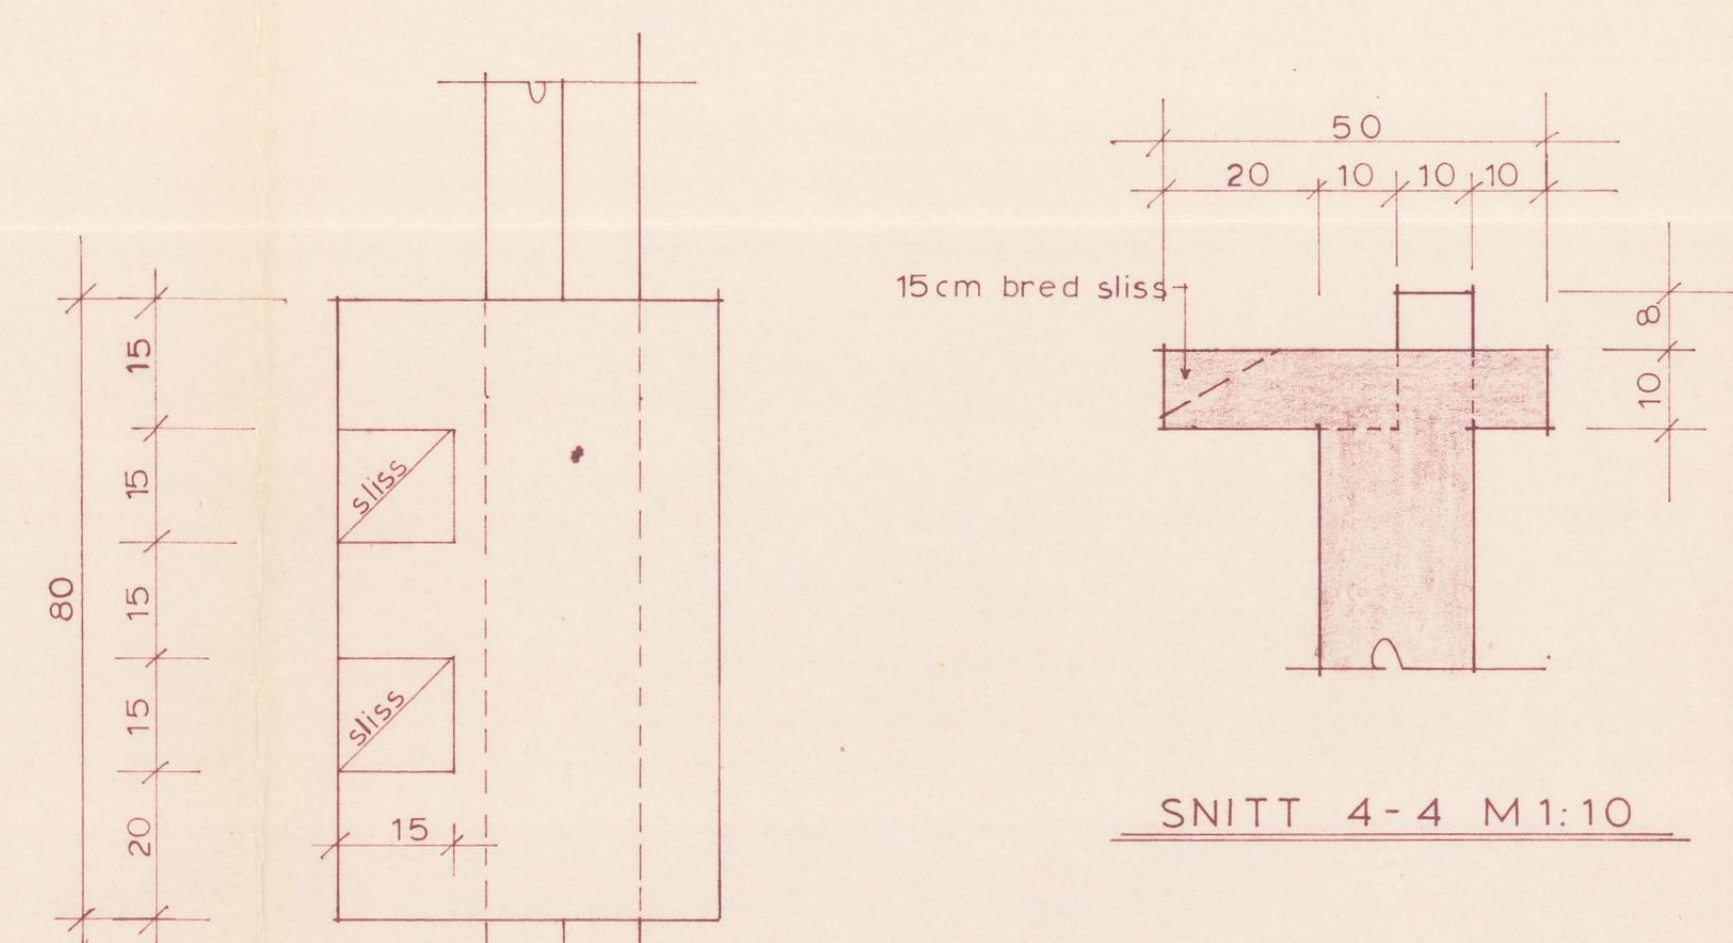


SNITT 4-4 M 1:10

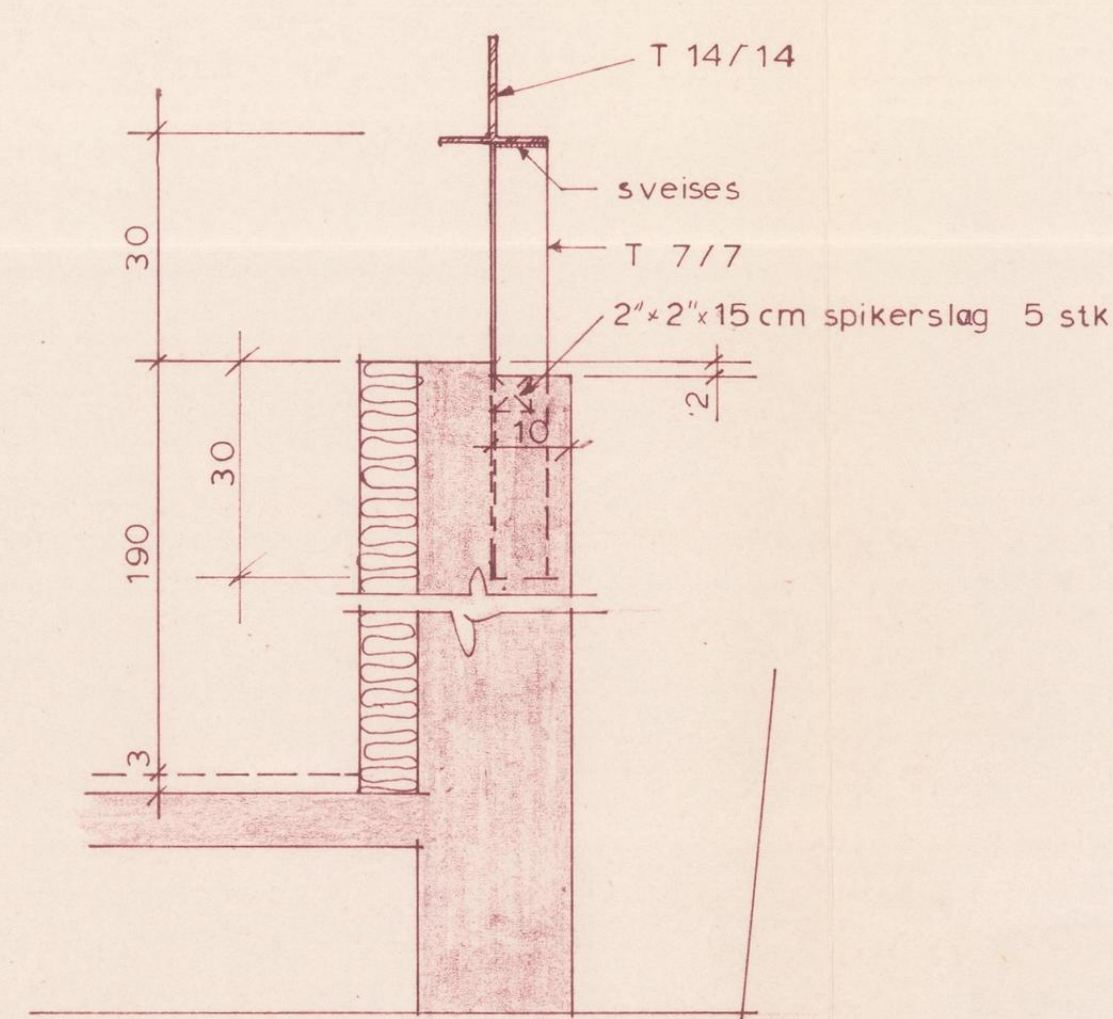


SNITT 3-3 M 1:10

PLAN AV PIPEFUNDAMENT M 1:10

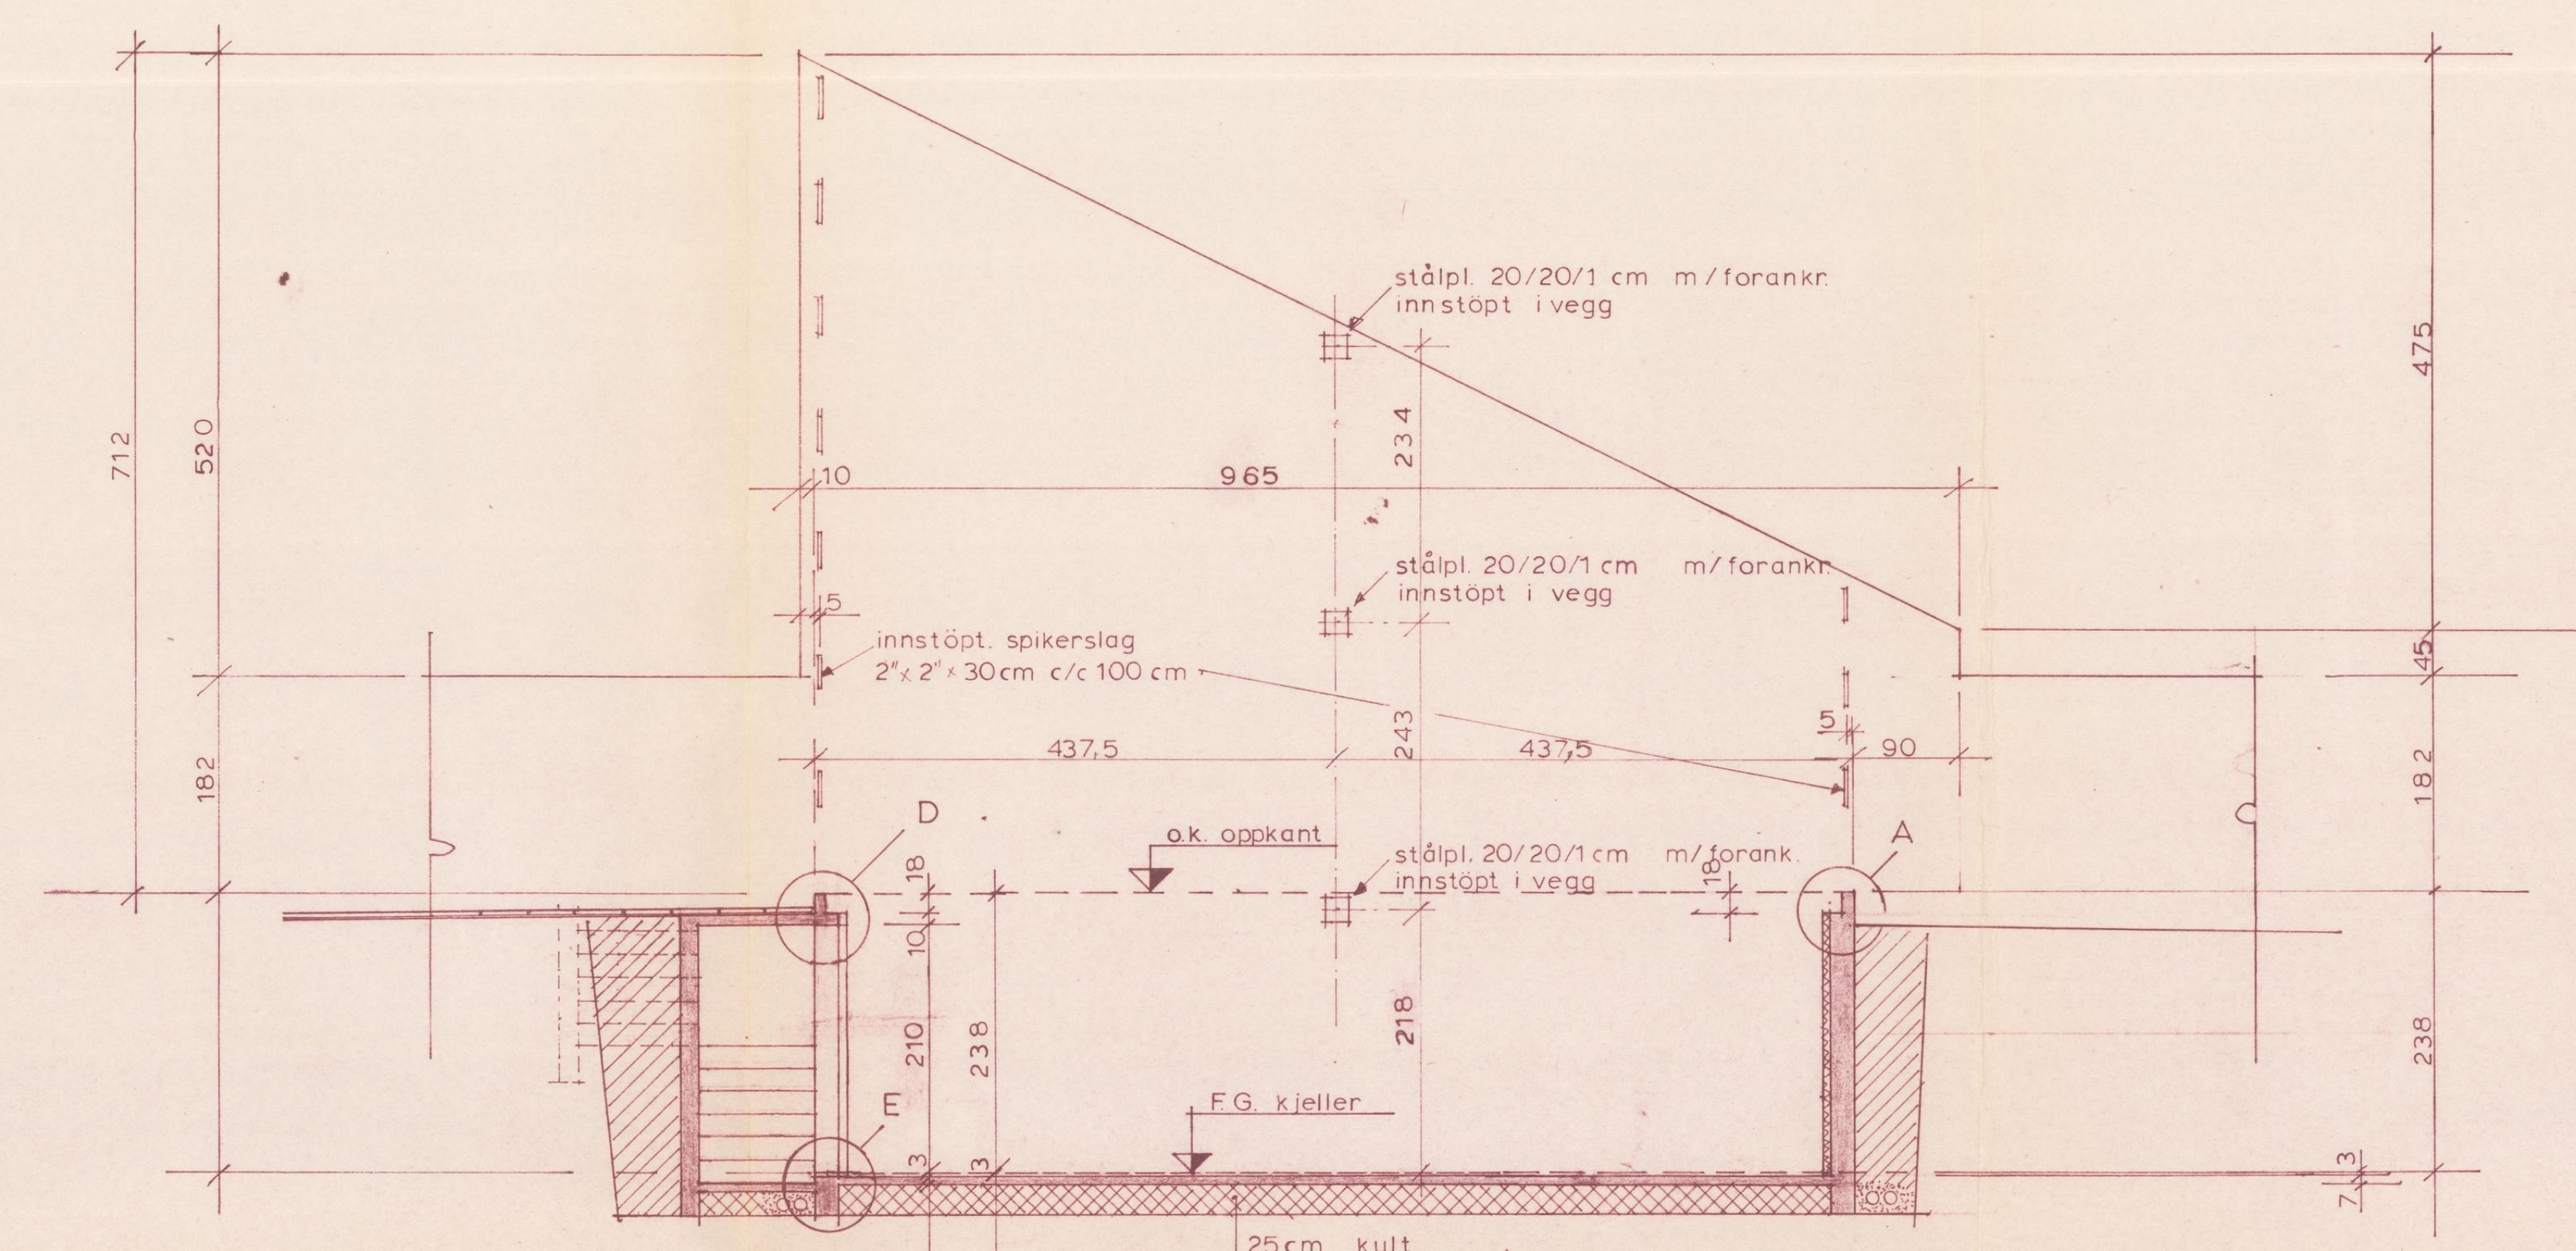


SNITT 2-2 M 1:50

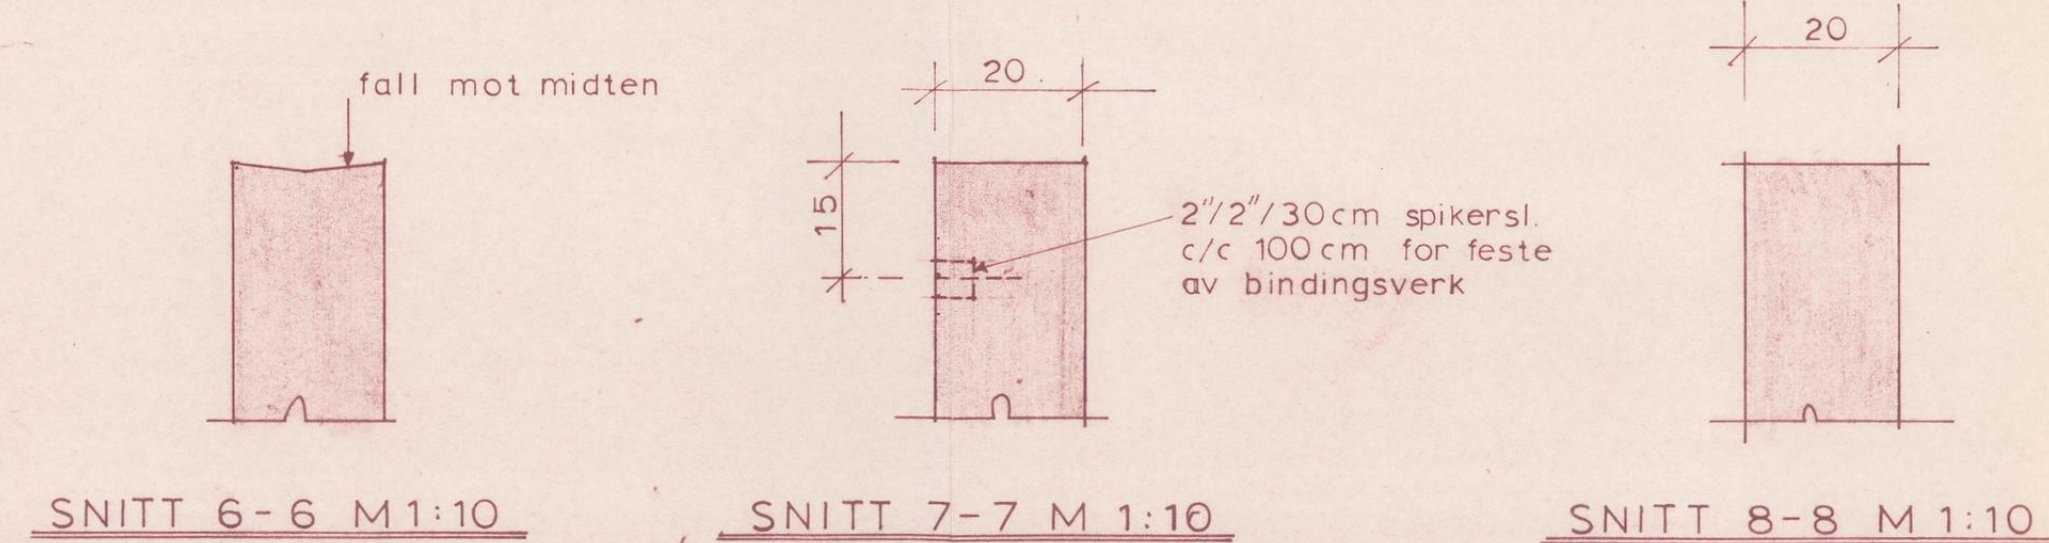

SNITT 6-6 M 1:10


SNITT 7-7 M 1:10

SNITT 8-8 M 1:10


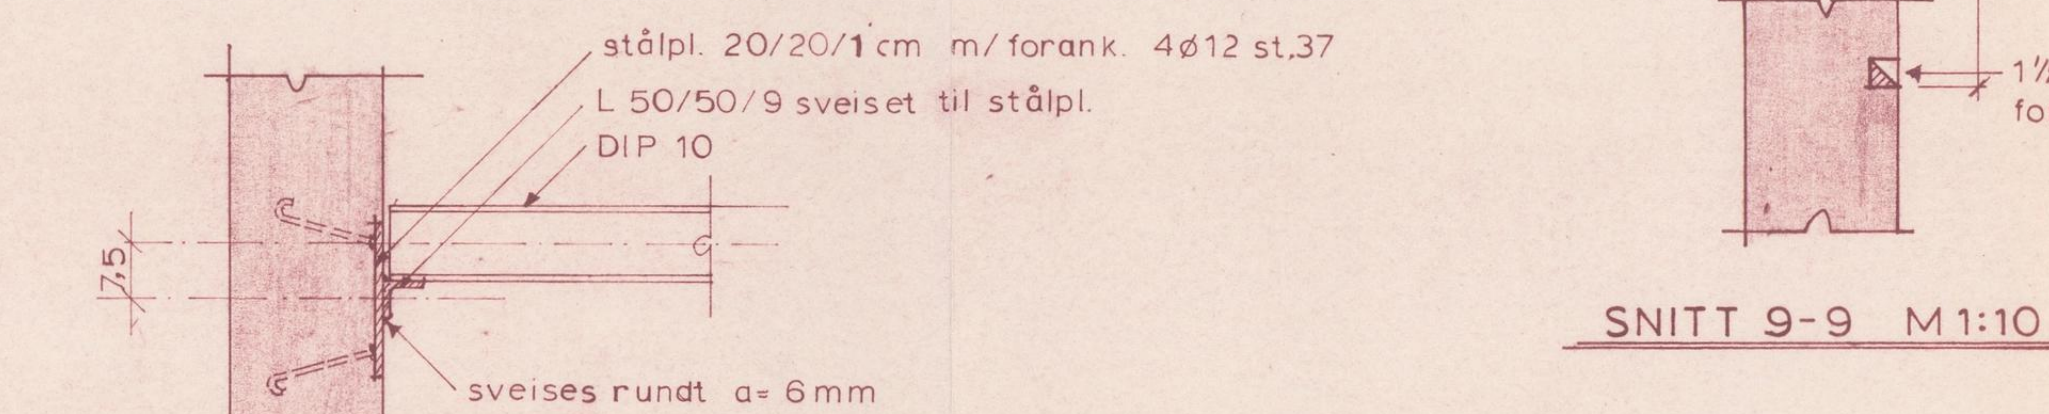


SNITT 9-9 M 1:10


OPPLEGG AV STÅLDR M 1:10

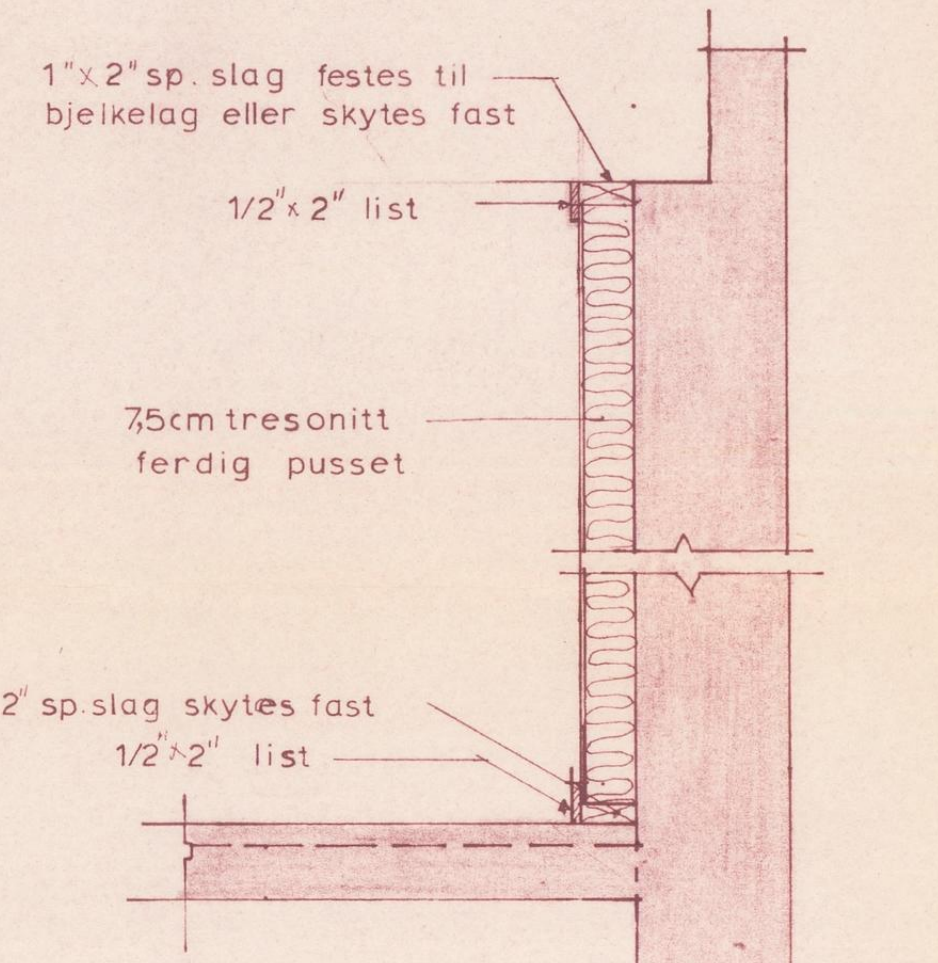


DETALJ F M 1:10

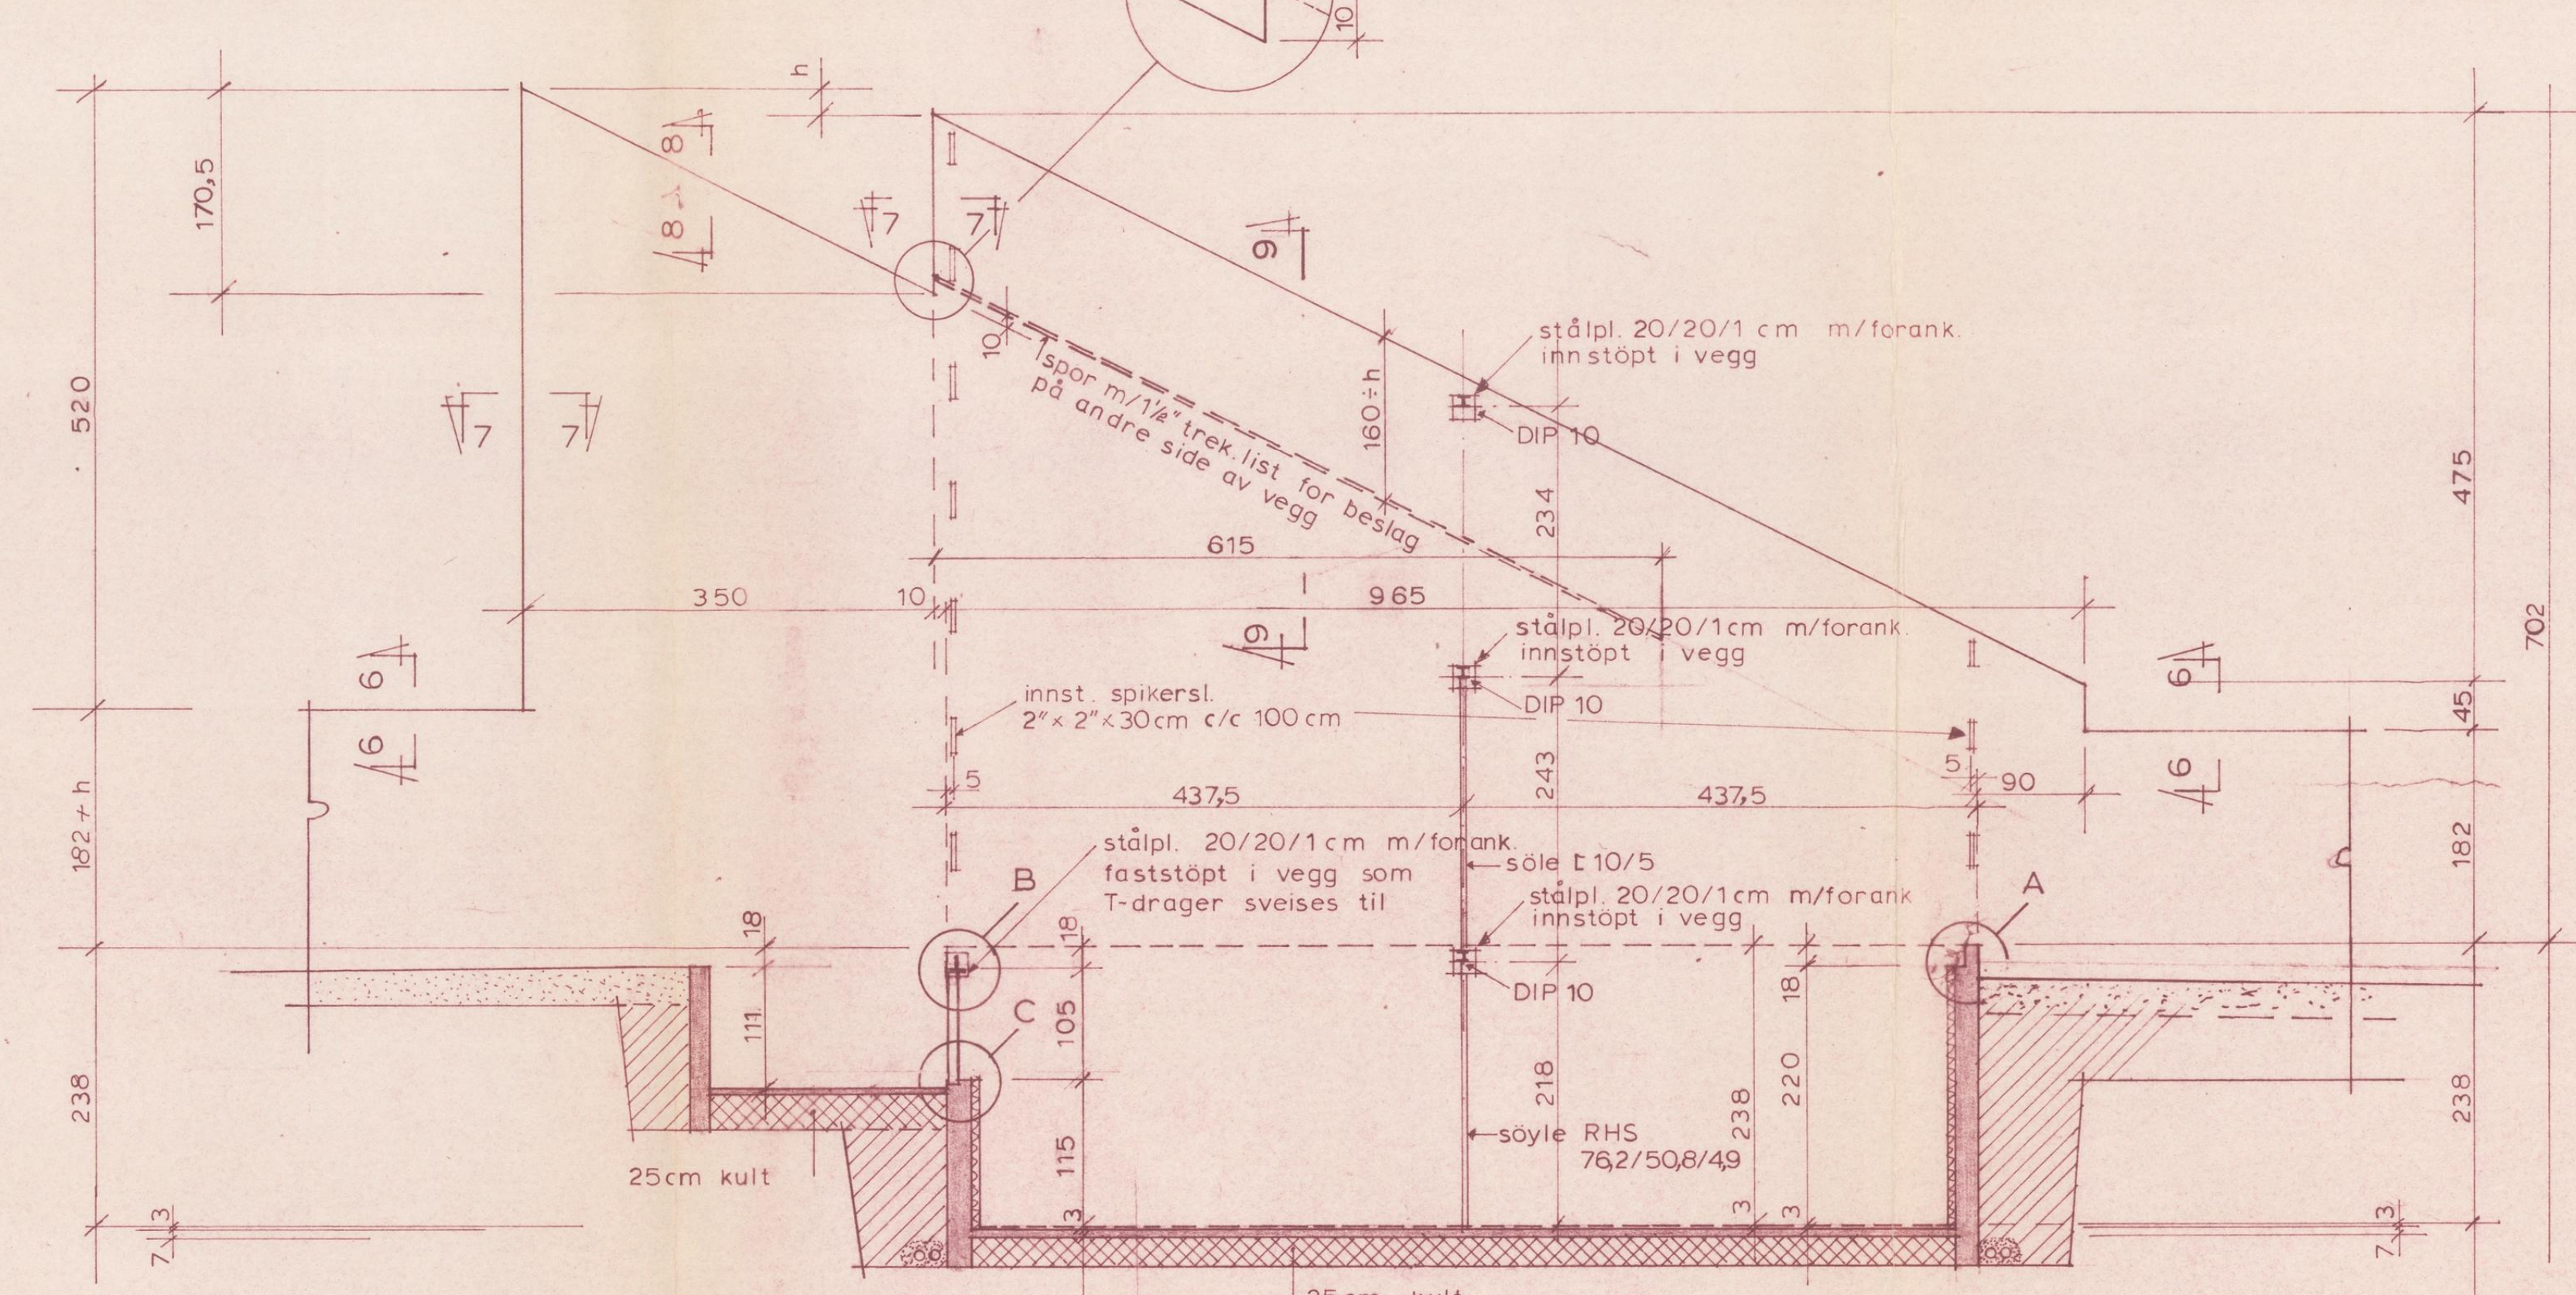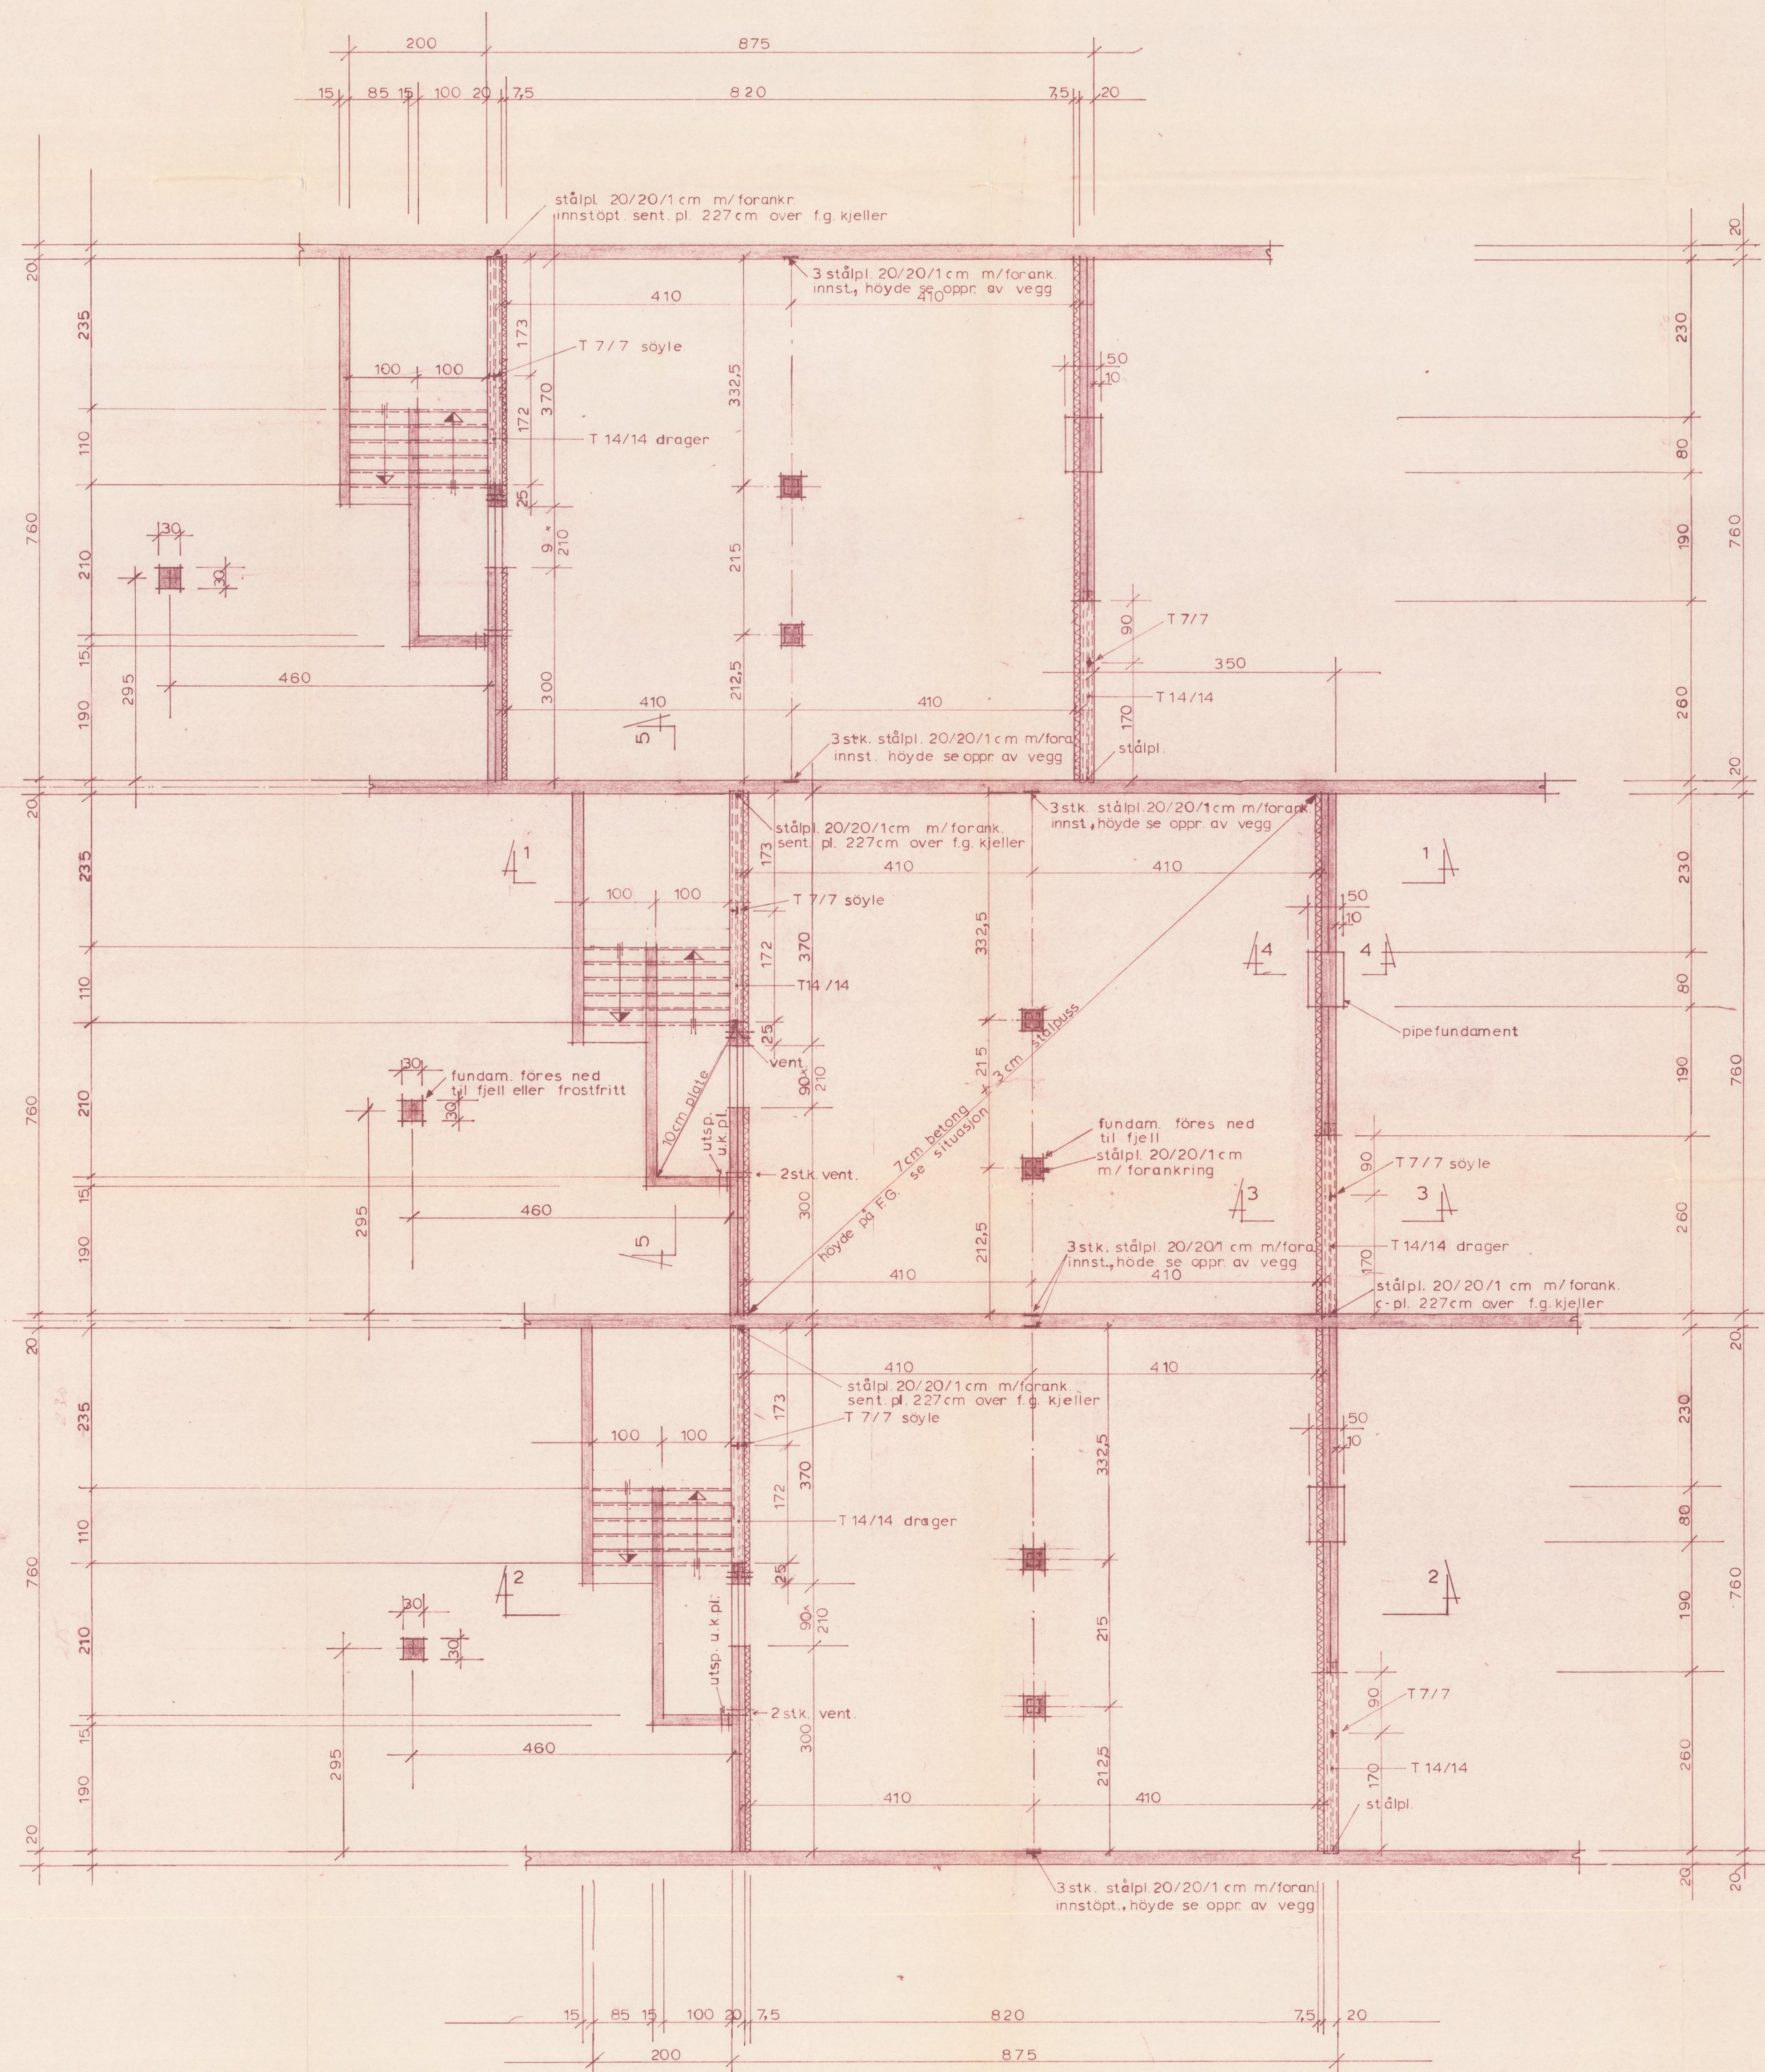


SNITT 1-1 M 1:50

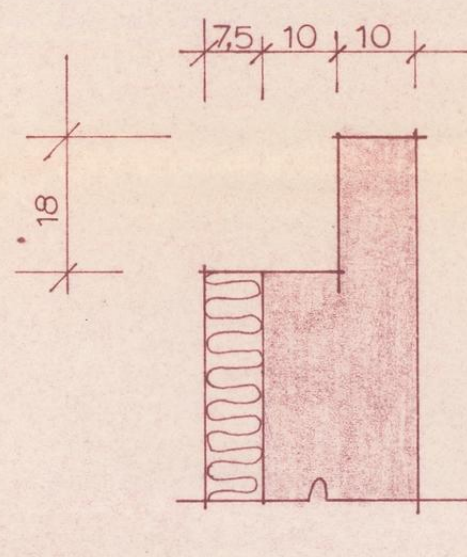


DETALJ A M 1:10

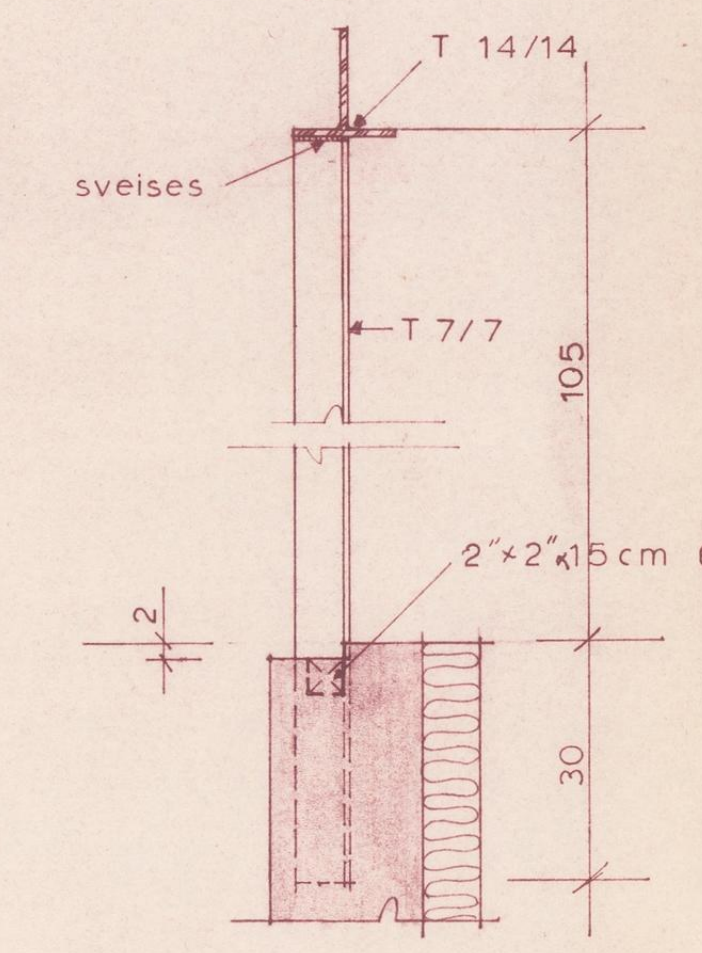

DETALJ B og C M 1:10

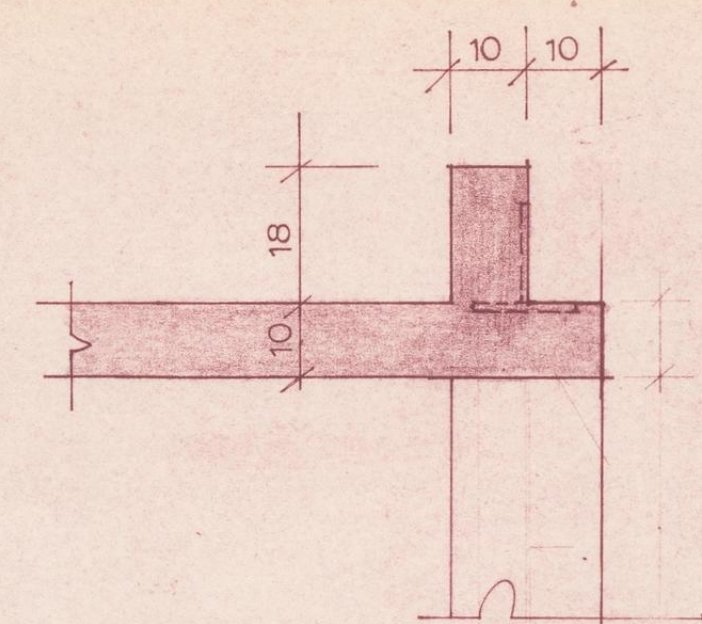

DETALJ D M 1:10

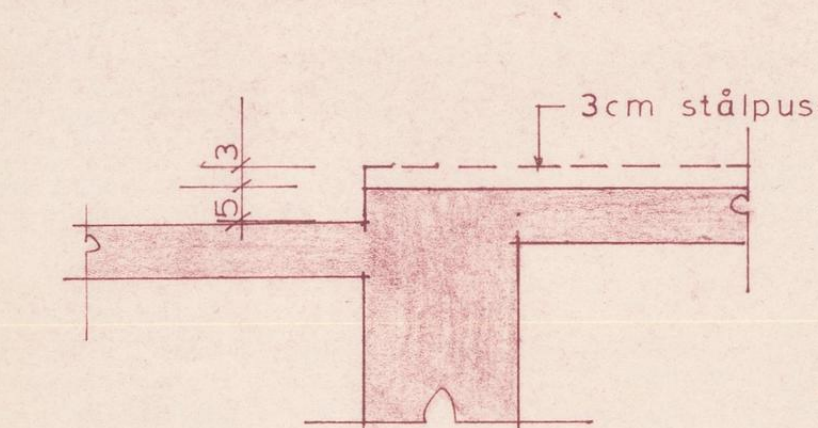


DETALJ E M 1:10


Godkjendt
Stavanger 18/9 70
Lars Vambheim

Stavanger Kommune
BYGNINGS- og
19 SEP 1970
Arkiv nr. 503.1 J. nr. 2910


4-9-70	innv. søylefundament flyttet	E.H.
4-9-70	ANBEFØRSEL	sign.
Tegn. nr. 112-07	Dato: 29-12-69	M 1:50
BOLIGBYGG		
BOLIGFELT MADLAMARKA SØR		
GRUNNMURER OG GOLF PÅ KULT MED DETALJER		
ING. LARS VAMBHEIM		
bygn. tekn. konsulent		
klubbgt. 1 Stavanger		
Tlf. 21455-27694		

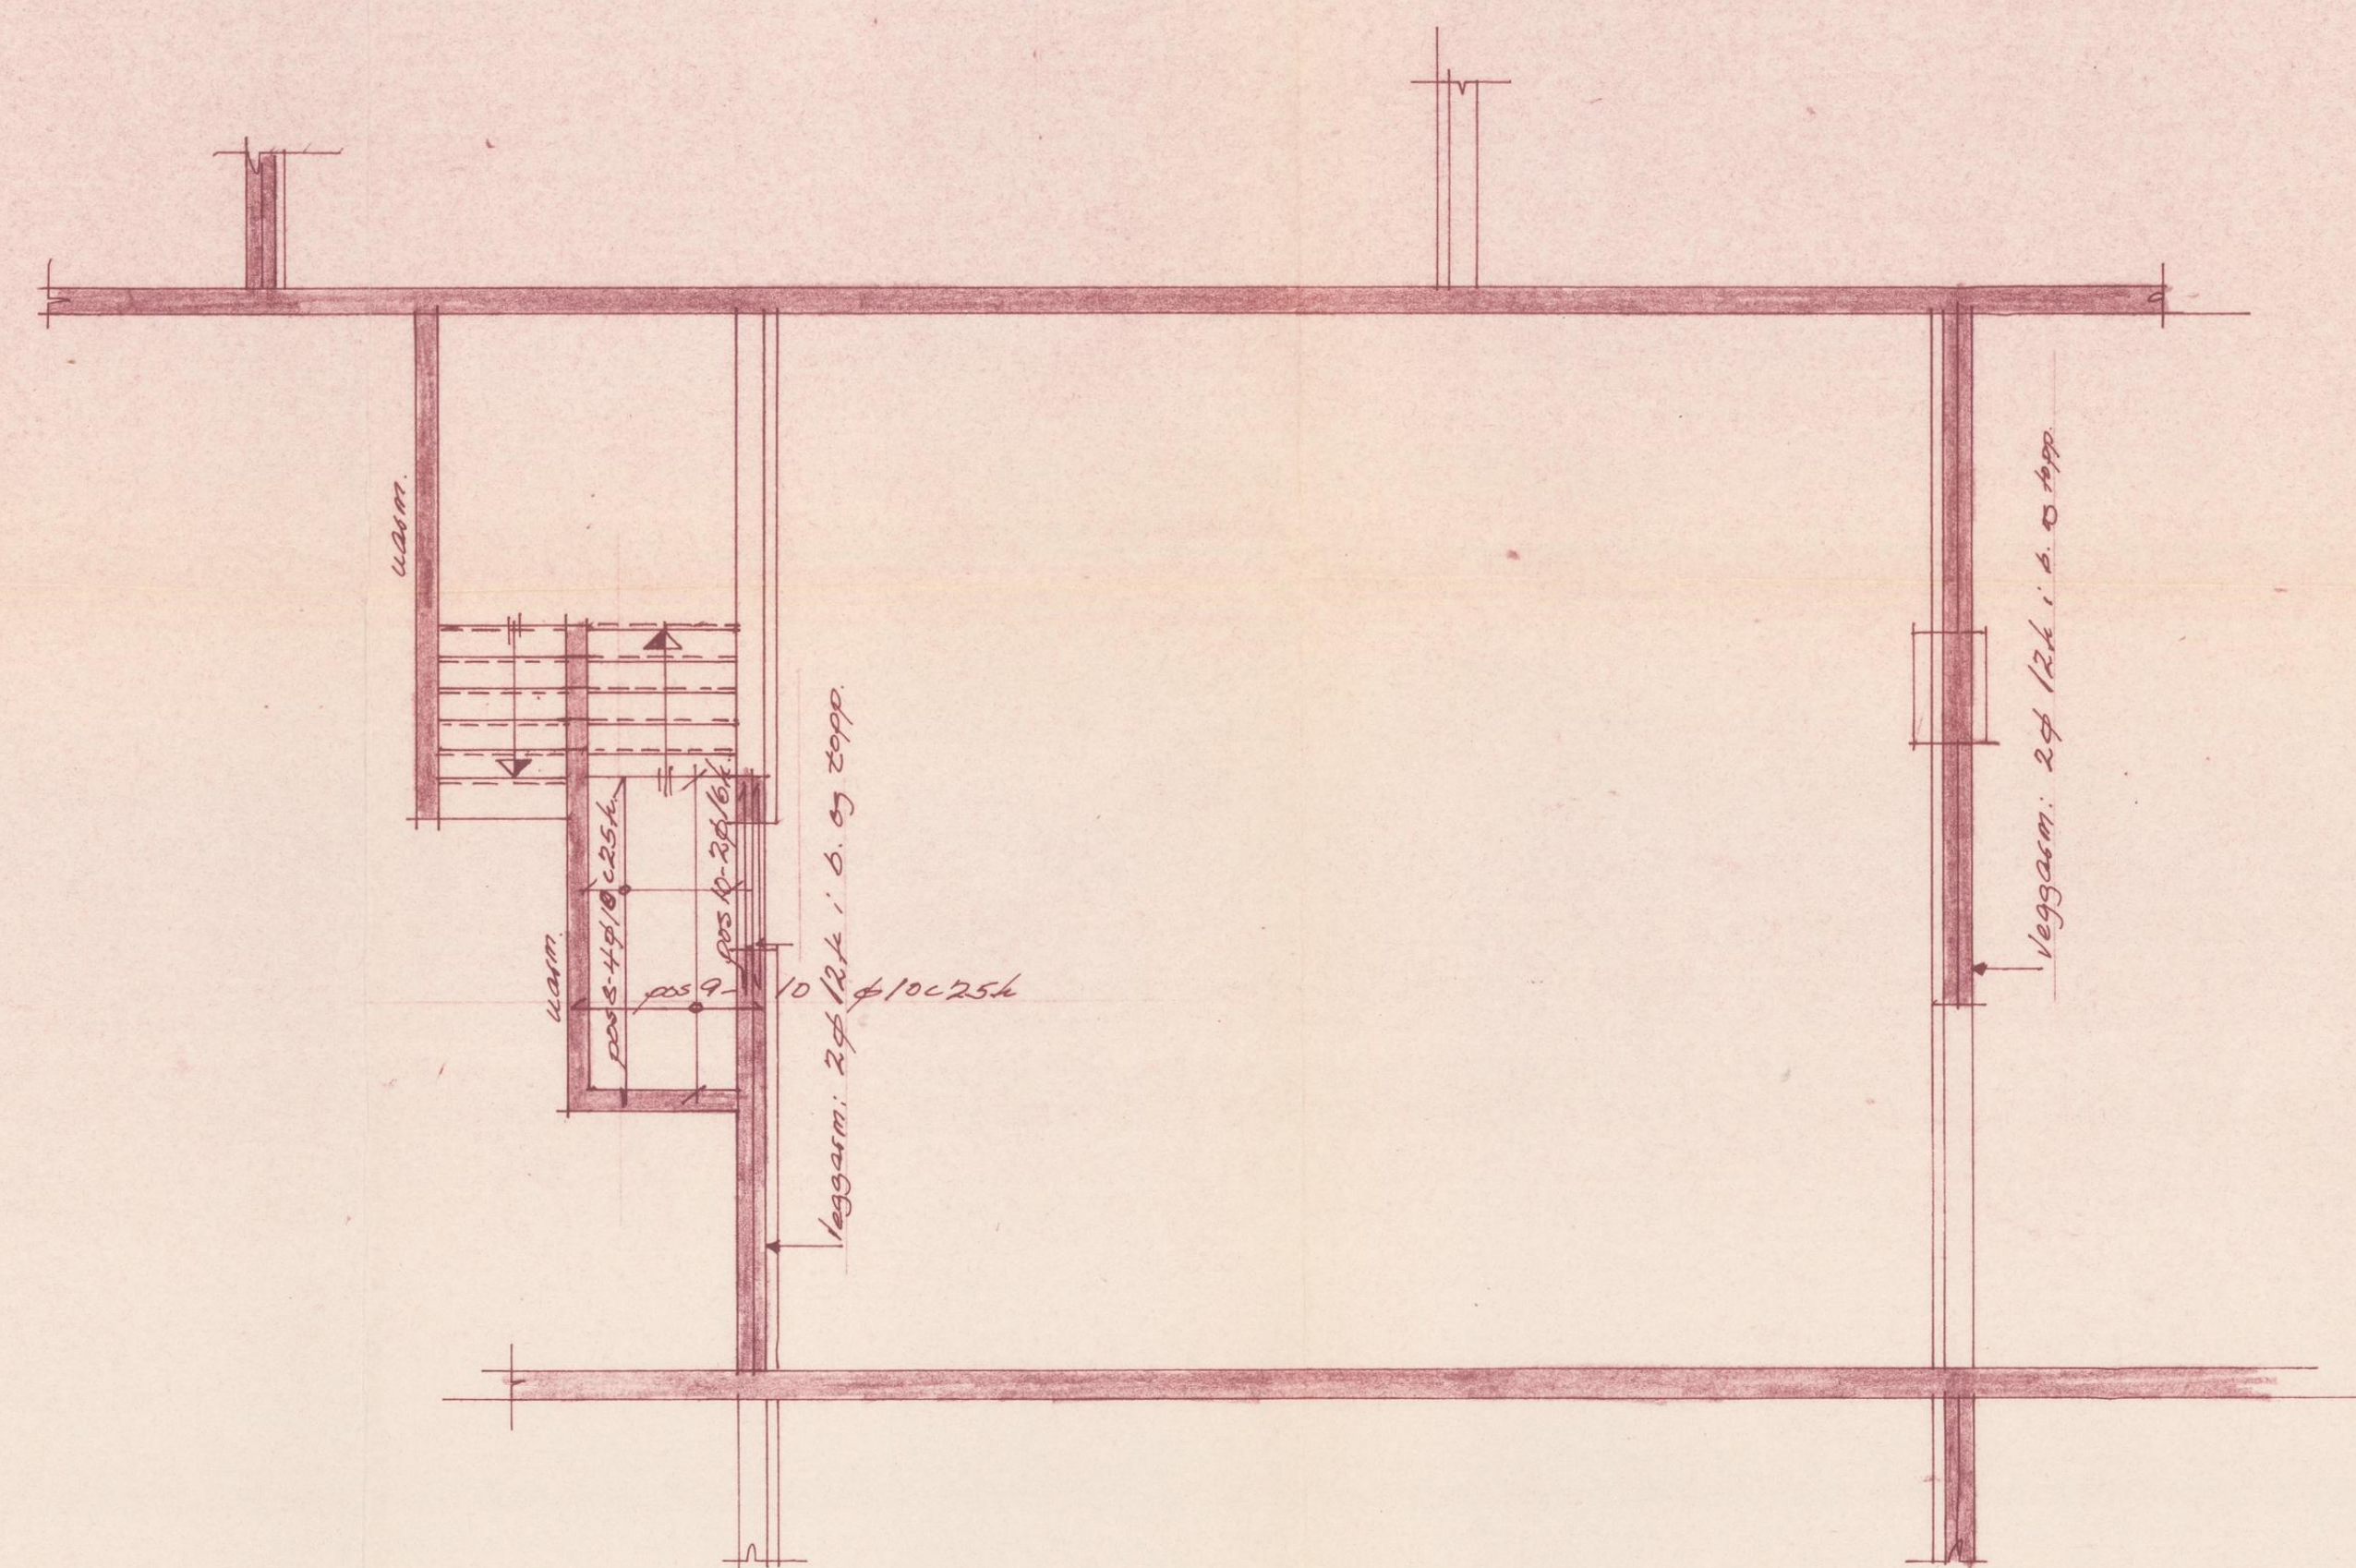


PLAN KJELLER M1:50

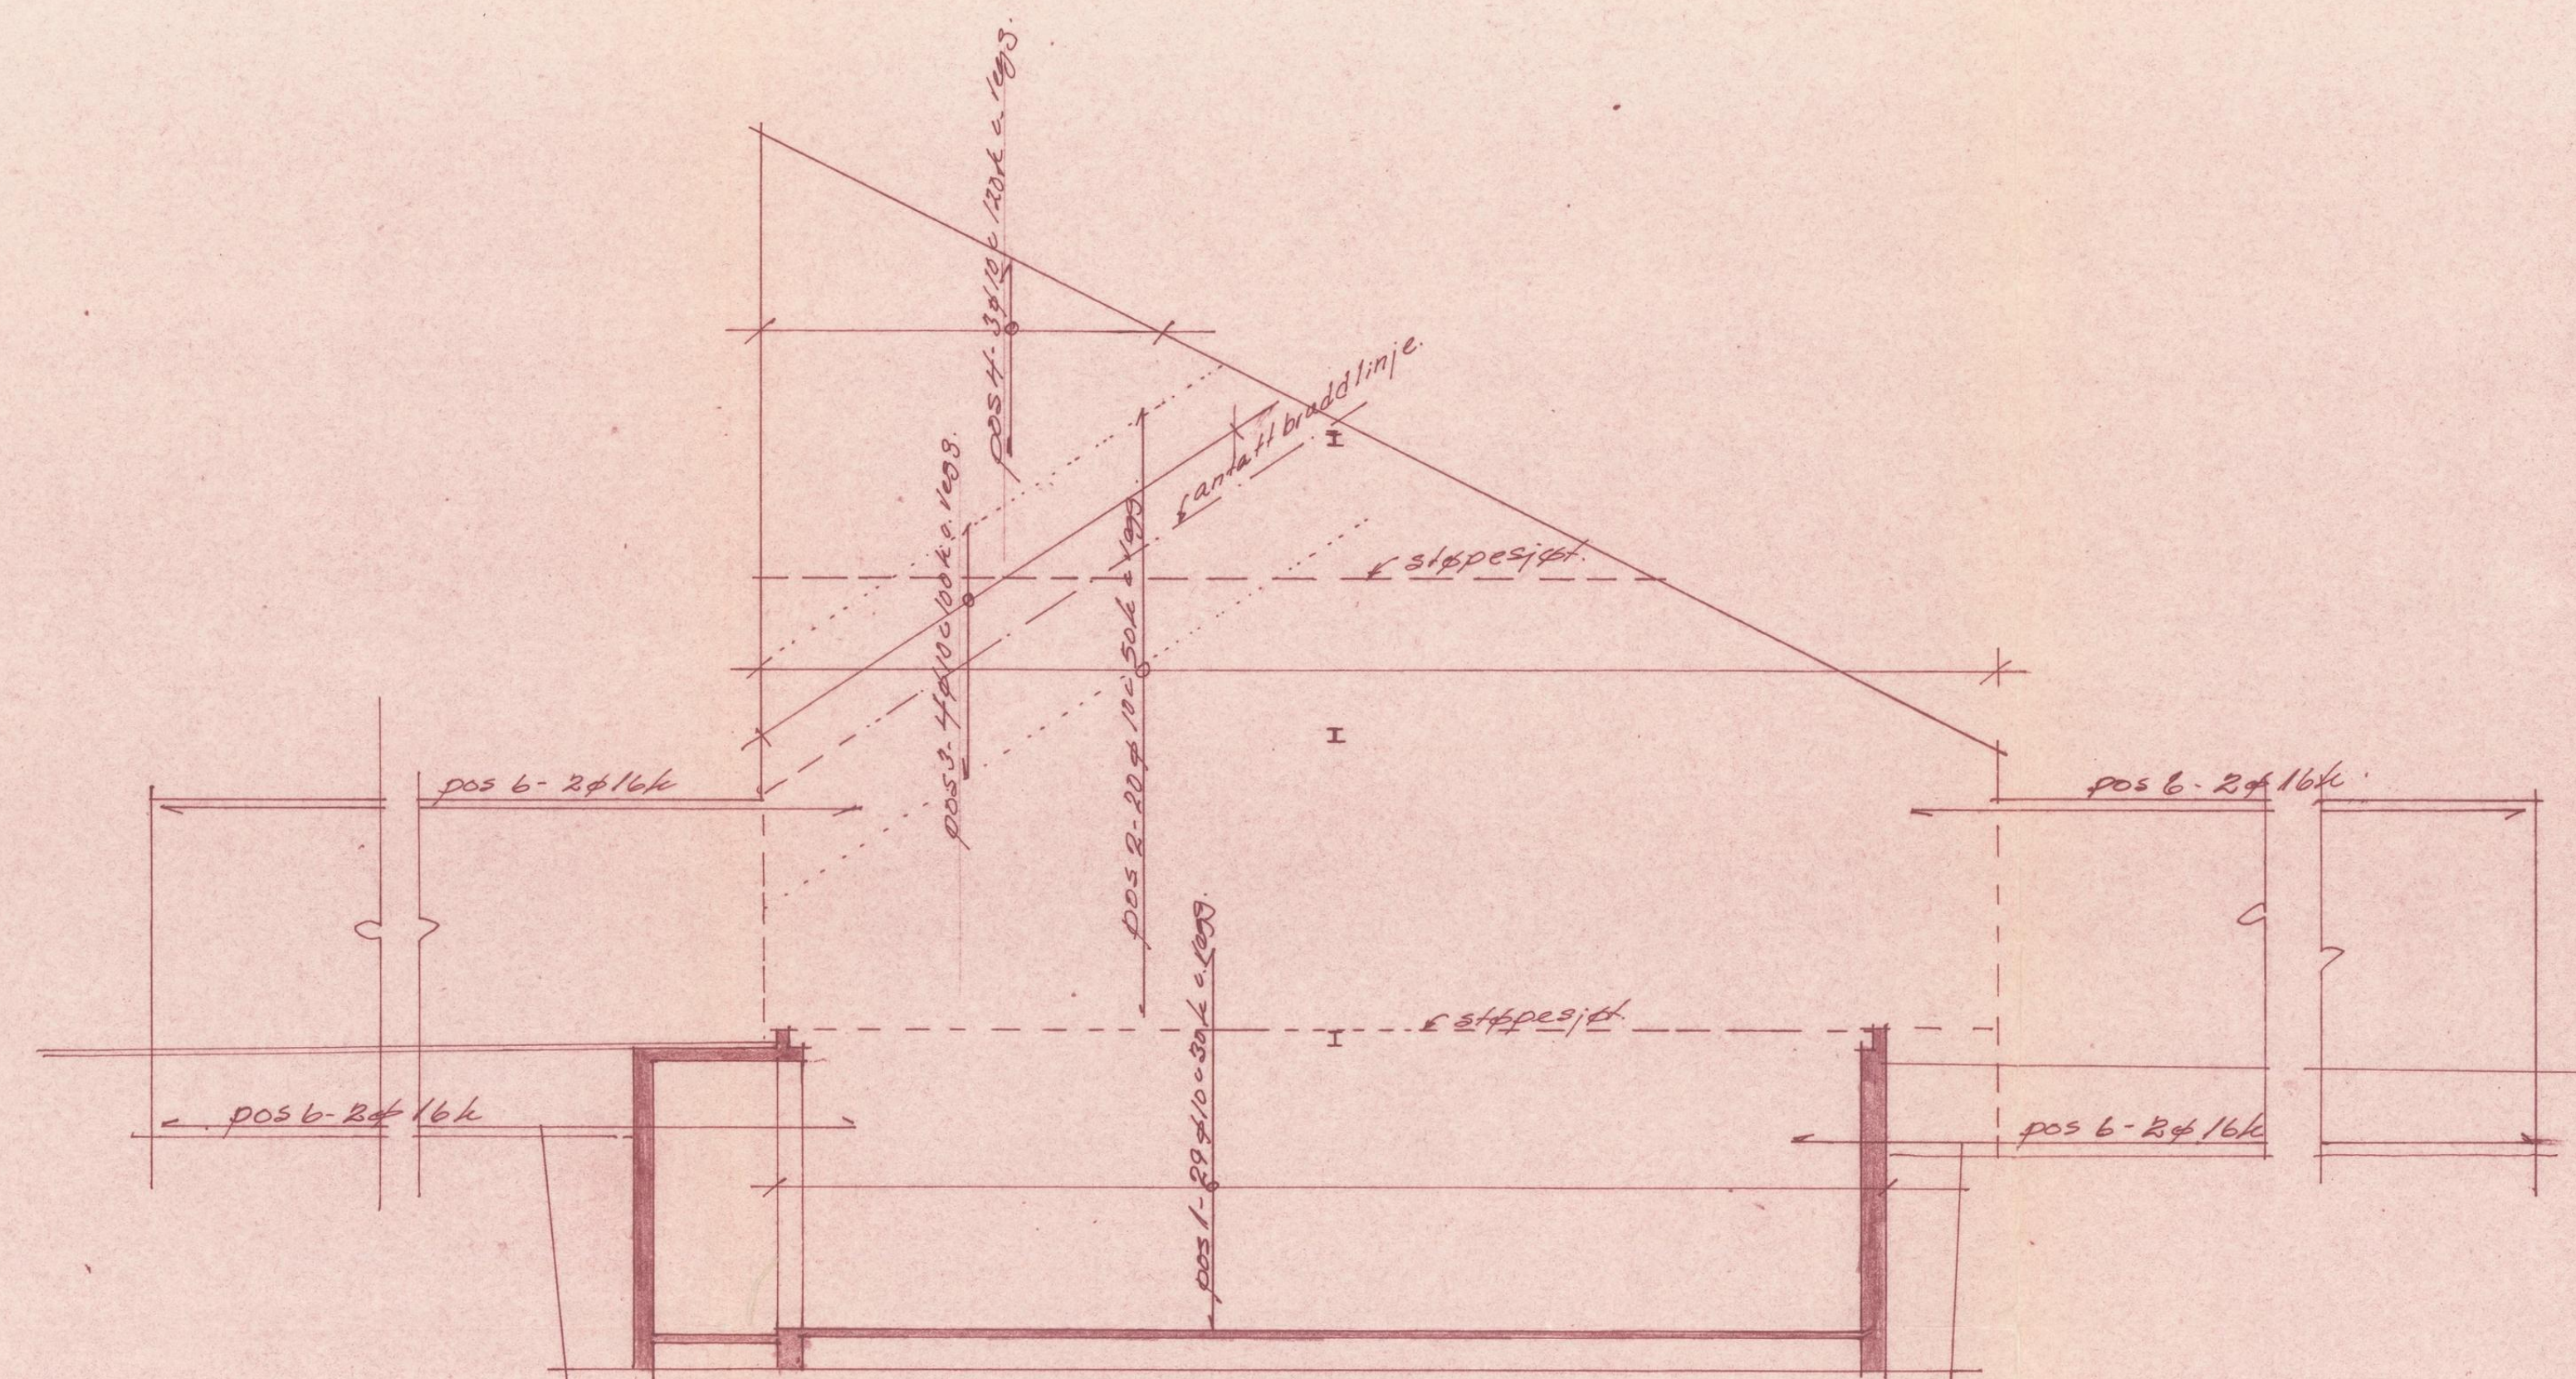

ARM. AV VEGG M1:50

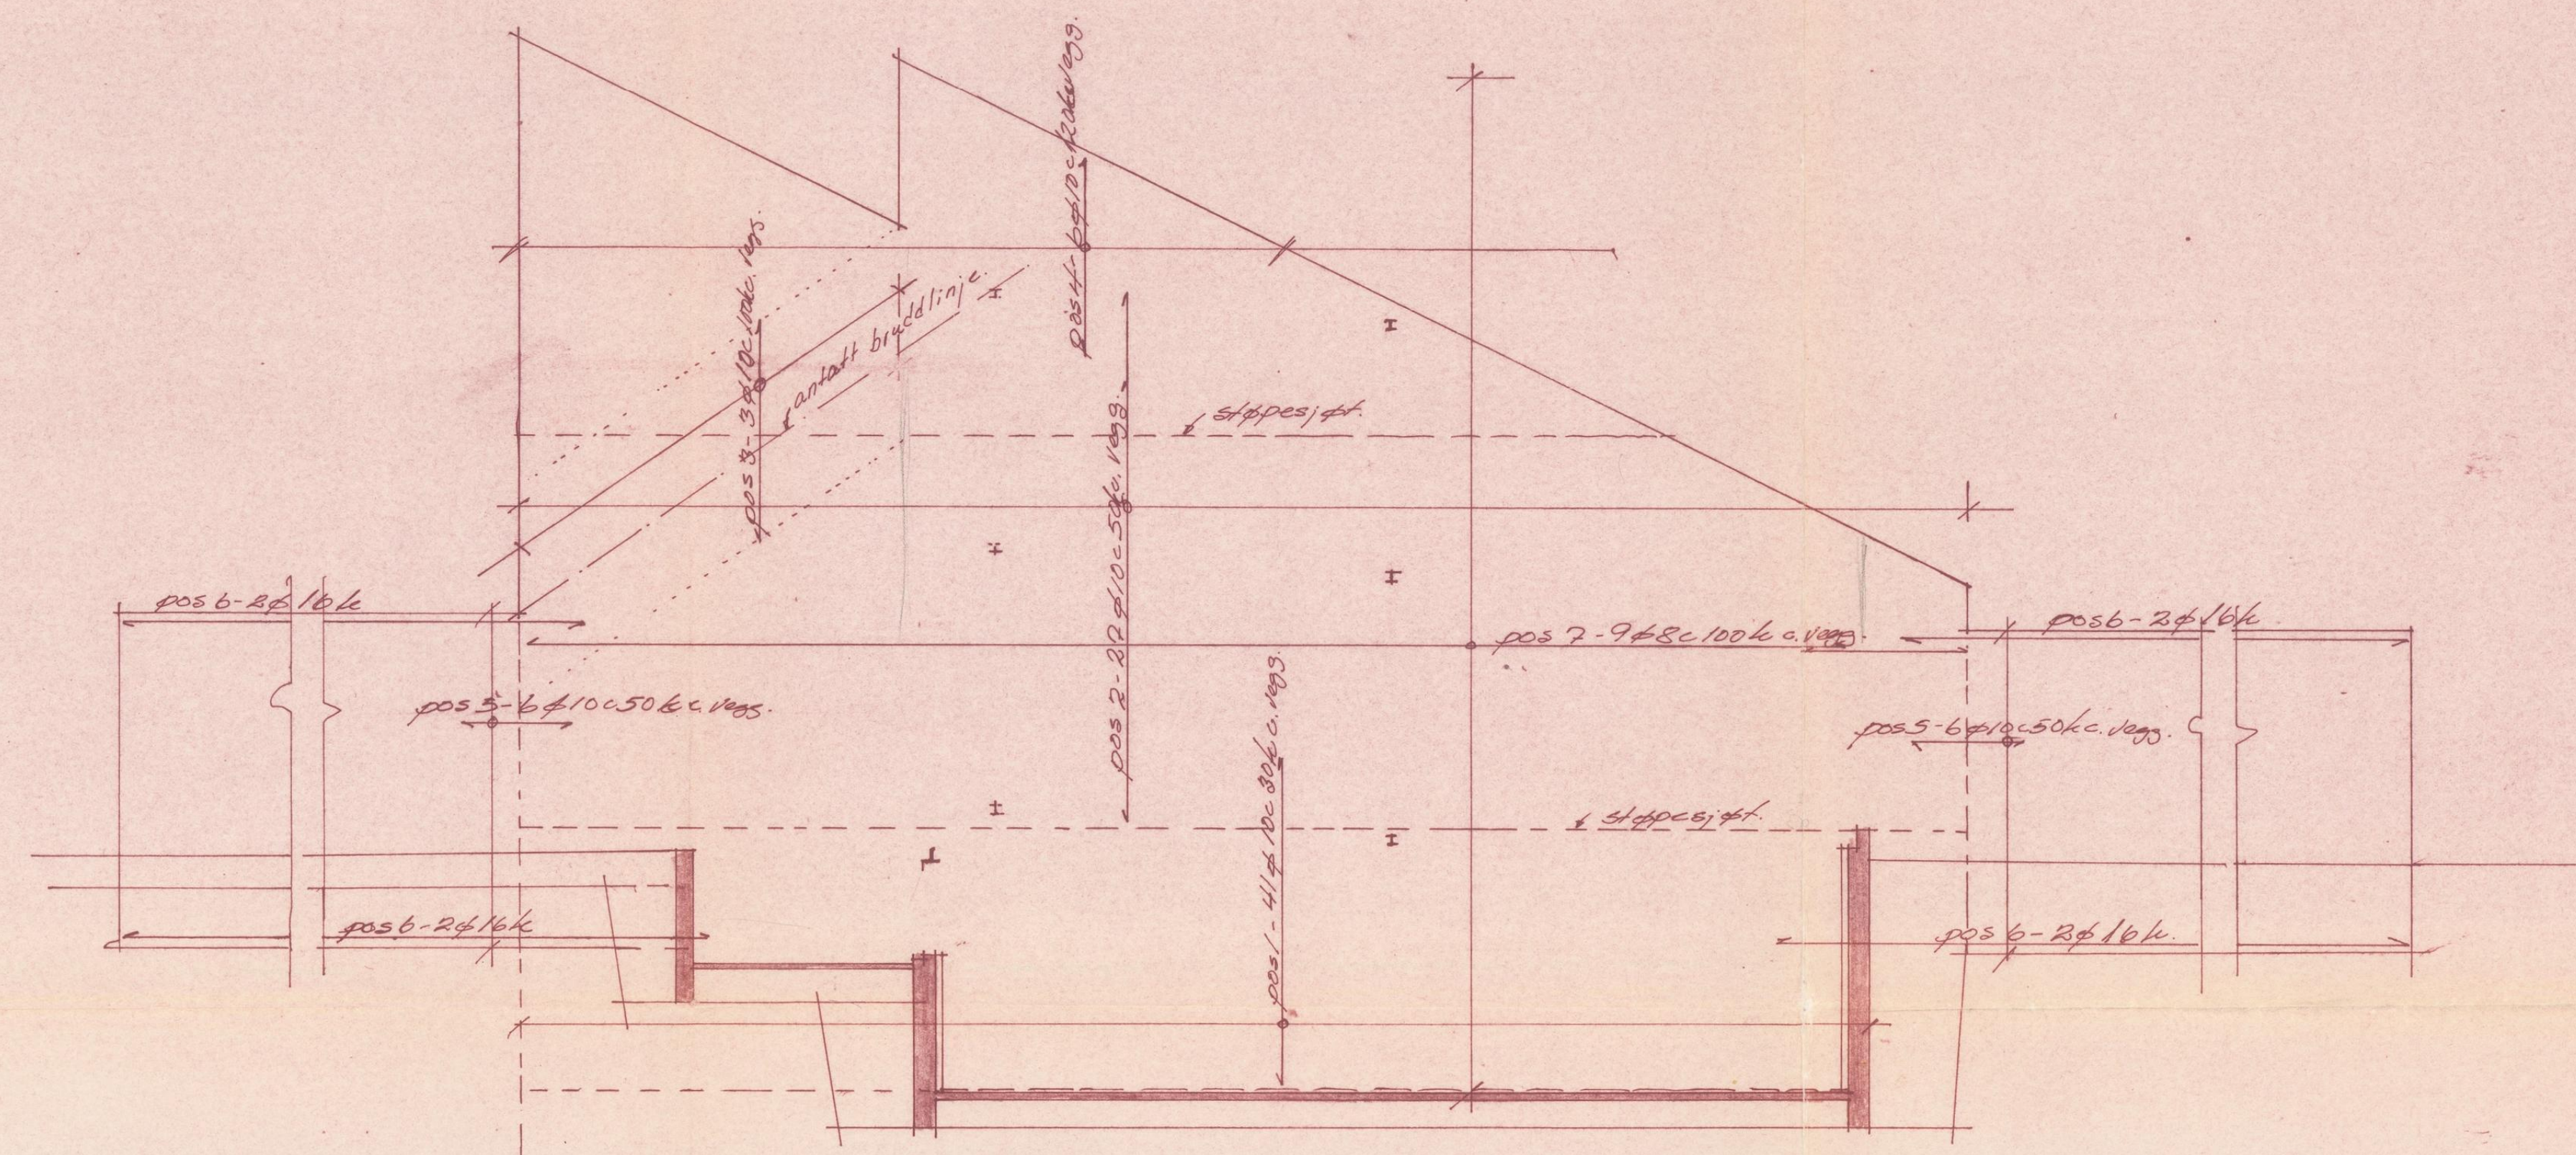

ARM. AV VEGGER M1:50

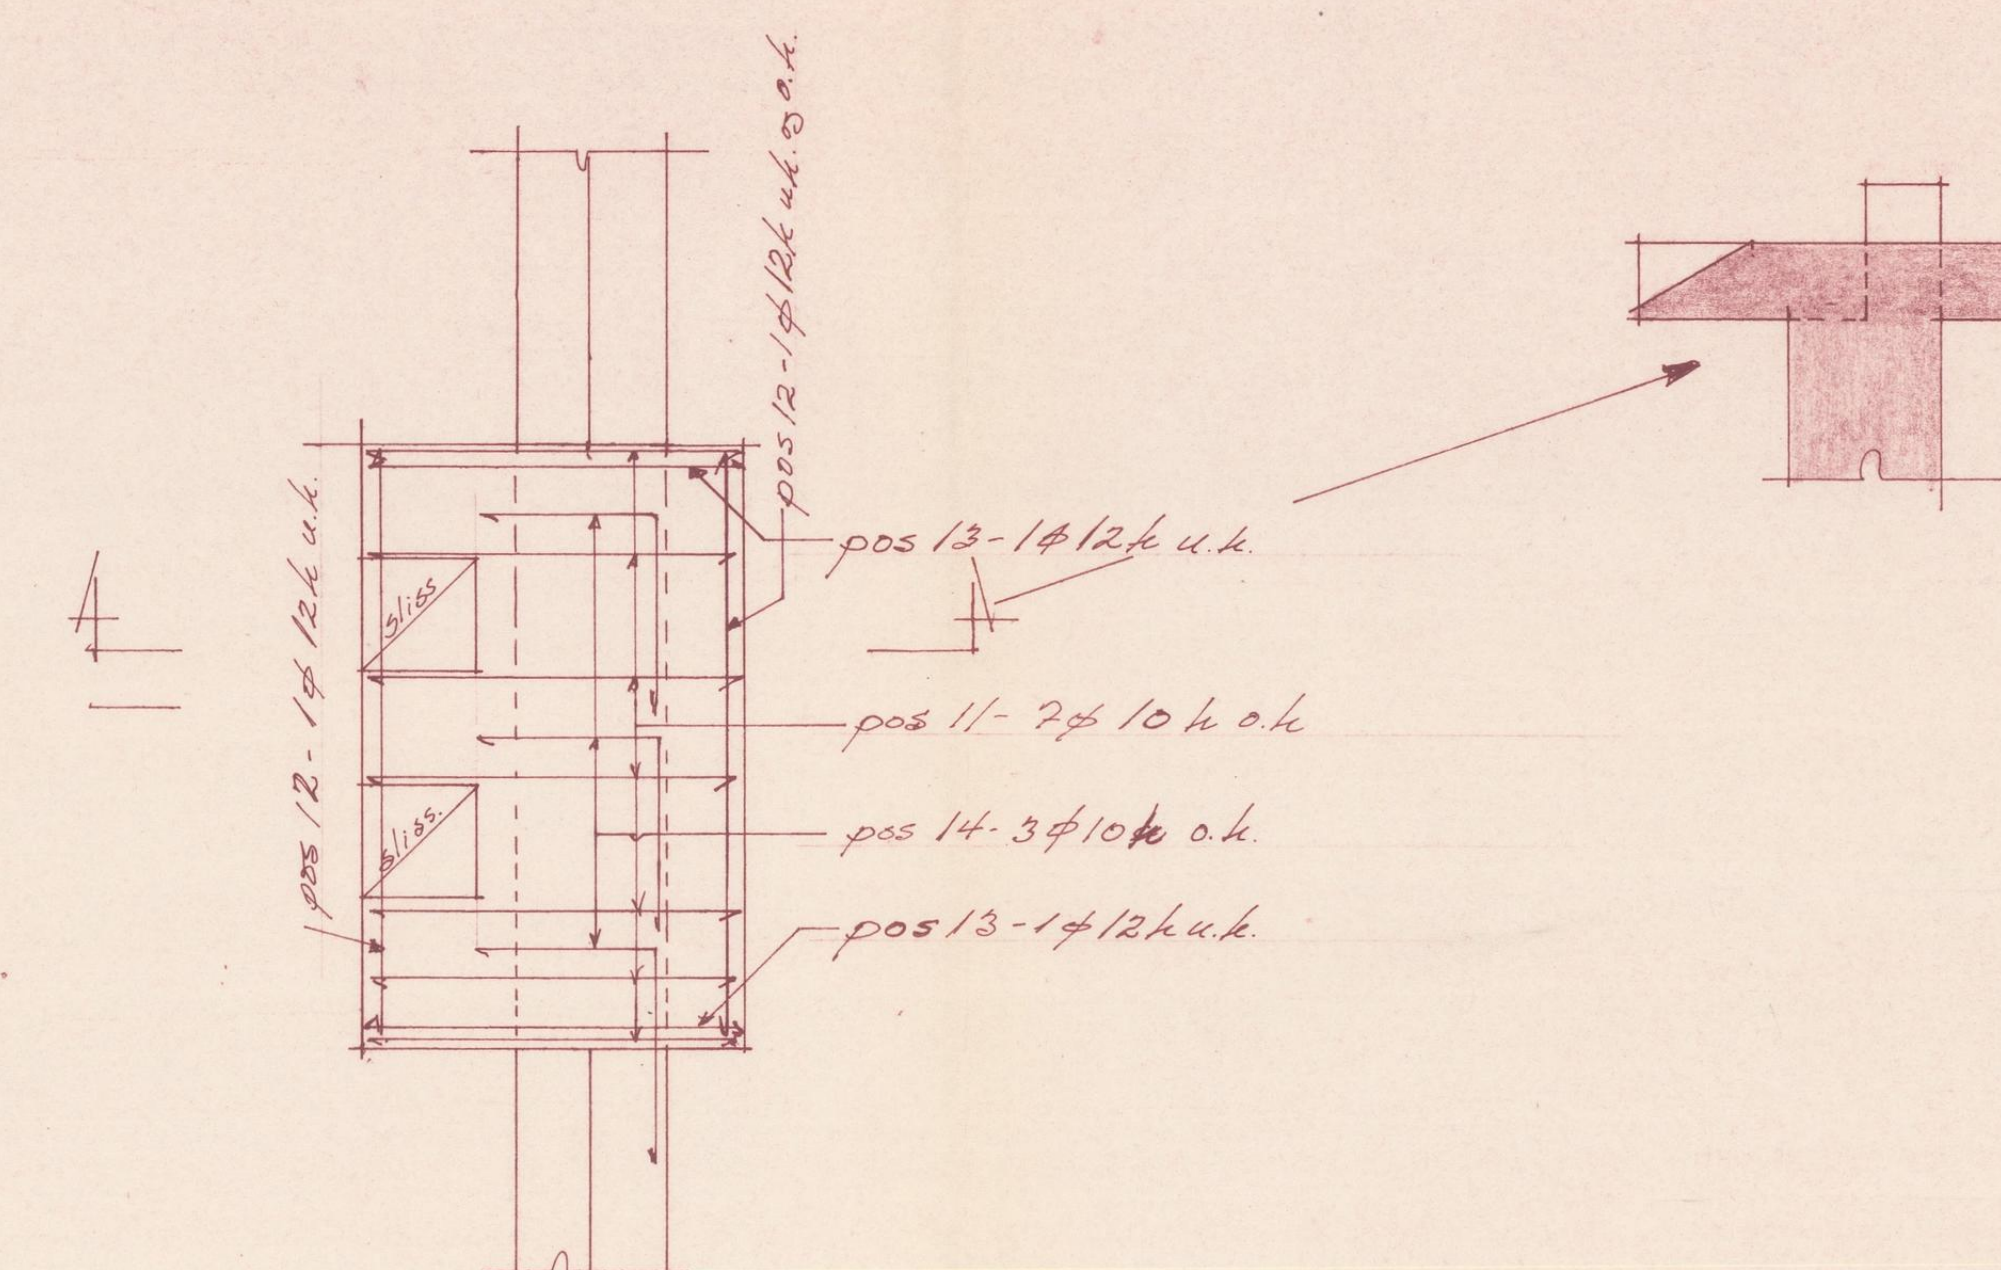

ARM. AV PEISFUNDAM. M1:10

Godkjendt.
Stavanger 8/9 70.
Lars Vambheim

Stavanger Kommune
BYGNINGSETATENE
7 JUN 1970

Arkiv nr. 503.1 1. m. 2795

dato:		endring:	sign:
Tegn. nr. 112 - 09	Dato: 1-9-70	M 1:50	E.M.
BOLIG - BYGG A/L			
BOLIGFELT MADLAMARK SØR			
ARM. AV VEGGER			
ING. LARS VAMBHEIM			
bygn. tekn. konsulent			
klubbgt. 1 Stavanger			
Tlf. 21455 - 27694			